

GLC

Thamesmead

Future Developments

This brochure describes schemes which comprise some of the future development of Thamesmead.

CONTENTS

AREA VIII EAST Page 3

Work on the second phase of the civil engineering work is programmed to start in October 1976 with a contract period of 29 months. The first of the housing contracts is programmed to start in Autumn 1977, with completion of all five contracts in 1981. The first dwelling completions are expected in Autumn 1979.

AREA IV G Page 9

The contract is programmed to start in December 1976 with a contract period of 18 months. First completions are expected within 12 months.

AREA III B and H Page 13


The order to commence was issued in April 1976 with a contract period of 36 months. First completions are anticipated after 18 months.

AREA III L Page 17

It is proposed that the contract will start during the first quarter of 1977 with a contract period of 28 months The first dwelling completions are anticipated in mid 1978.

AREA X Page 21

Work on the advance civil engineering contract is programmed to start in August 1976, with a contract period of 19 months. The first of the housing contracts is programmed to start in March 1977, with completions of all four contracts at the end of 1980.

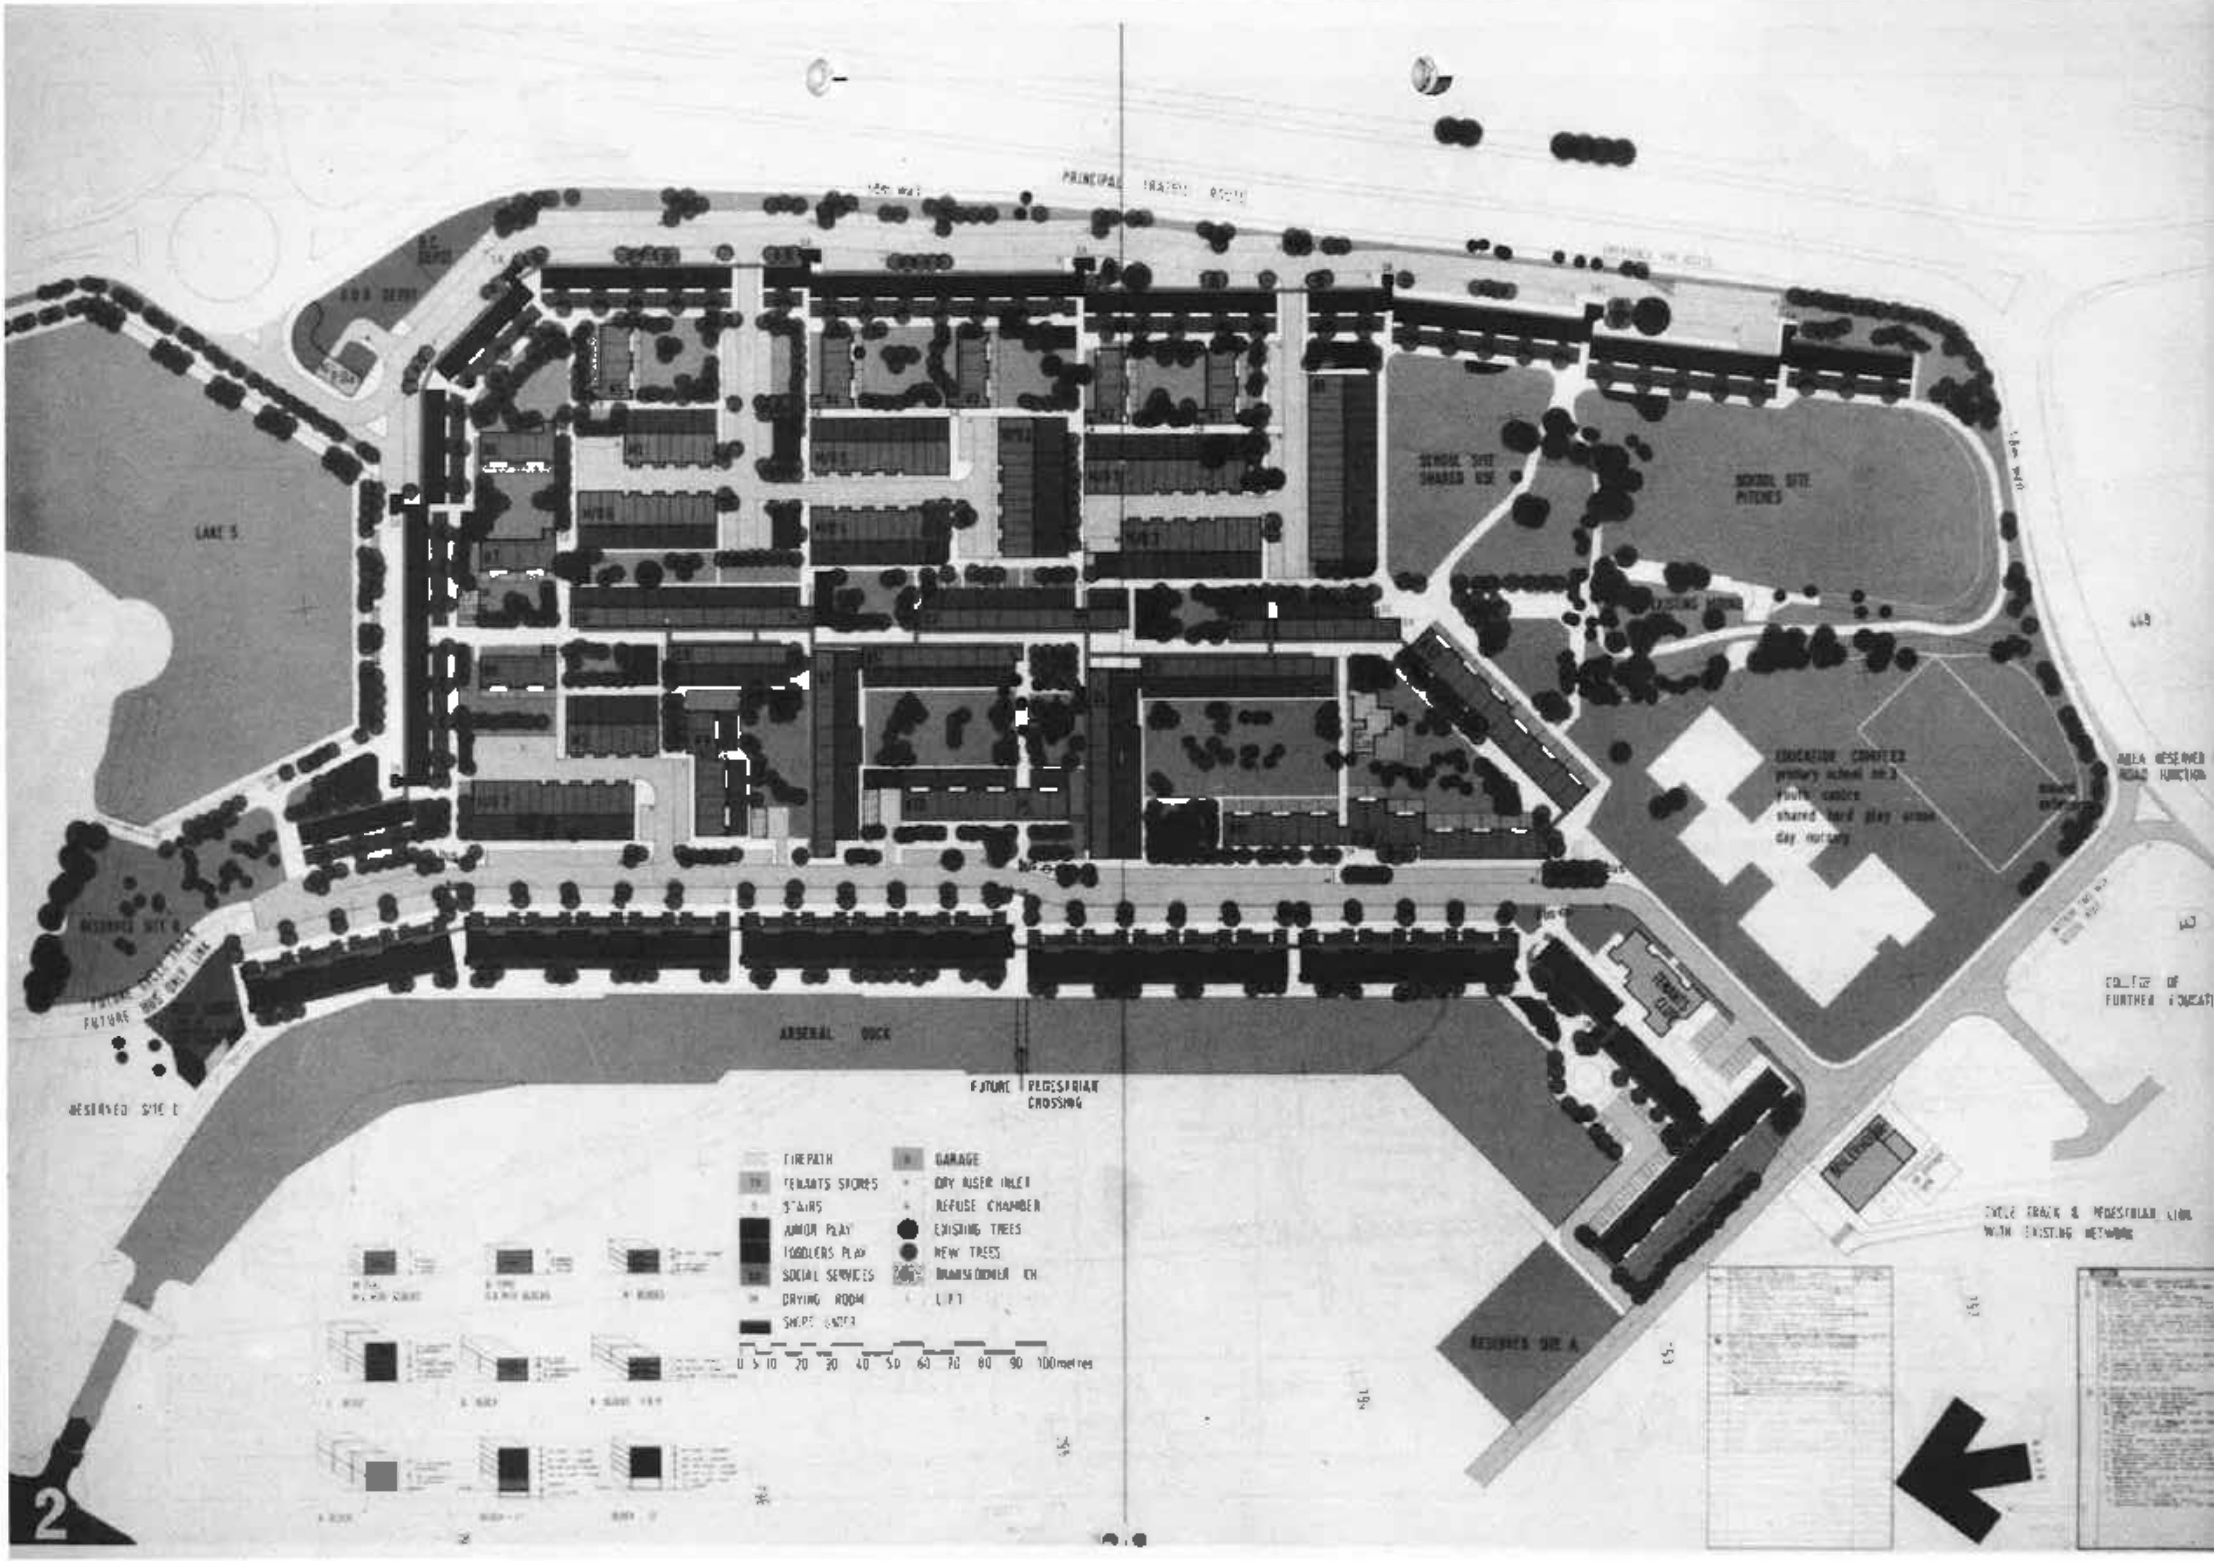
LAKE 5
ARSENAL DOCK
FUTURE PEDESTRIAN CROSSING
RESERVED SITE A
RESERVED SITE C
SCHOOL SITE SHARED USE
SCHOOL SITE PITCHES
EDUCATION CENTRES
primary school on 3
public access
shared hard play areas
day nursery
AREA RESERVED ROAD JUNCTION
TENNIS CLUB
CYCLE TRACK & PEDESTRIAN LINK WITH EXISTING NETWORK
FIREPATH
TENANTS STORES
STAIRS
JUNIOR PLAY
TODDLERS PLAY
SOCIAL SERVICES
DRYING ROOM
GARAGE
DRY RISER INLET
REFUSE CHAMBER
EXISTING TREES
NEW TREES
TRANSFORMER KIOSK
LIFT
0 5 10 20 30 40 50 60 70 80 90 100metres
2

AREA VIII EAST

The Thamesmead Town Map was approved by the Minister of Housing Local Government in 1969 and this indicated an area lying to the north of Plumstead Road and west of Griffin Manorway known as Area VIII to be allocated partly for residential and partly for industrial purposes. Some public open space and private playing fields were also indicated. However, more detailed studies into the actual land use allocations indicated that there would be certain planning advantages in developing Area VIII primarily for residential purposes. The presence of the Arsenal Dock and canal in this area provided an attractive feature which could be retained and would provide a setting of great amenity value to a wholly residential area. The main objectives in preparing the layout for this area were:

a) to provide an environment human in scale with variety of interest and the maximum amount of accommodation in houses with their own gardens and

b) to retain the basic strong and simple linear framework, common to the other areas, which gives the town its recognisable form and distinctive profile whilst serving the more utilitarian function of protection from traffic noise and from climatic conditions on such an exposed site.

Although the design of the site had to be revised to conform with the financial restraint imposed by the Housing Cost Yardstick, it has been possible to retain much of the best of the original scheme, that the 5 storey single aspect block along the principal traffic road, providing shelter from traffic noise to the larger houses and the elderly persons' accommodation, which are grouped around green squares and pedestrian areas of the site. The 4 storey block fronting the Arsenal Dock, introduced to exploit the amenity value of the waterway has also been retained.

The scheme provides 917 dwellings, 50% being low rise houses and 3 storey flats and the remainder 4/5 storey linear blocks of maisonettes and flats. 425 of the low rise dwellings have gardens. All the buildings have been designed to be constructed in traditional form and materials, that is, light, predominantly yellow shade brickwork, brown roofs and wall tiles and timber window frames.

Analysis

Gross site area	15.86 hectares (39.66 acres)
Housing area	12.20 hectares (30.52 acres)
Population	3419
Density	258 persons per hectare (103 ppa)

Block/ Storey	Persons/Dwellings								Totals	
	OPD II	IIF	IVM	IVF	VM	VH	VIH	VIIH	Dwellings	Persons
J 4-5	40	52							92	184
K 4			69		69				138	621
L 5			98	49	97				244	1073
M 3						16			16	80
M/O 3						56	30		86	460
N 3	134	74						7	215	465
Q 3			73	37					110	440
O 3							16		16	96
									917	3419

Garages - 7 Car Ports - 118
Open Parking - 670 Future Parking - 99
Total provision for 894 vehicles, which is 97.5% of all dwellings.



AREA VIII EAST LAYOUT



A local district heating scheme will provide heating and hot water from its own boiler room. Natural gas will be used as fuel in the first instance but the boilers are designed to allow a change to oil at a later date if required. There will be hot water radiators in contrast to the warm air system in Areas I, II and IIIA and D.

A local shopping centre consisting of a supermarket, launderette and newsagent, with additional bays suitable for expansion will be provided in the initial contract. Other facilities include a tenants' clubroom, an old people's club, an old peoples sitting room, and sites are reserved for works depots and a social services office for the London Borough of Greenwich.


Residents will use the Main Health Centre to be built in the Central Area.


Education facilities are provided by a 2 form entry primary school (No. 3) sited within the Area. The use of the primary school open space (1.2 hectares/3 acres) will be shared with the general public, and this together with .55 hectare (1.38 acres).of an existing well treed mound satisfies the need of the open space provision.

An advance civil engineering contract will open up the site and provide the basic services for the development. This will be followed by five separate housing contracts and a further contract for the construction of the boiler house. To achieve the fastest possible start on the housing work, the engineering works will be phased to ensure early commencements of the following housing work.


MAISONETTES
OVERLOOKING LAKE 5

MEWS
HOUSING

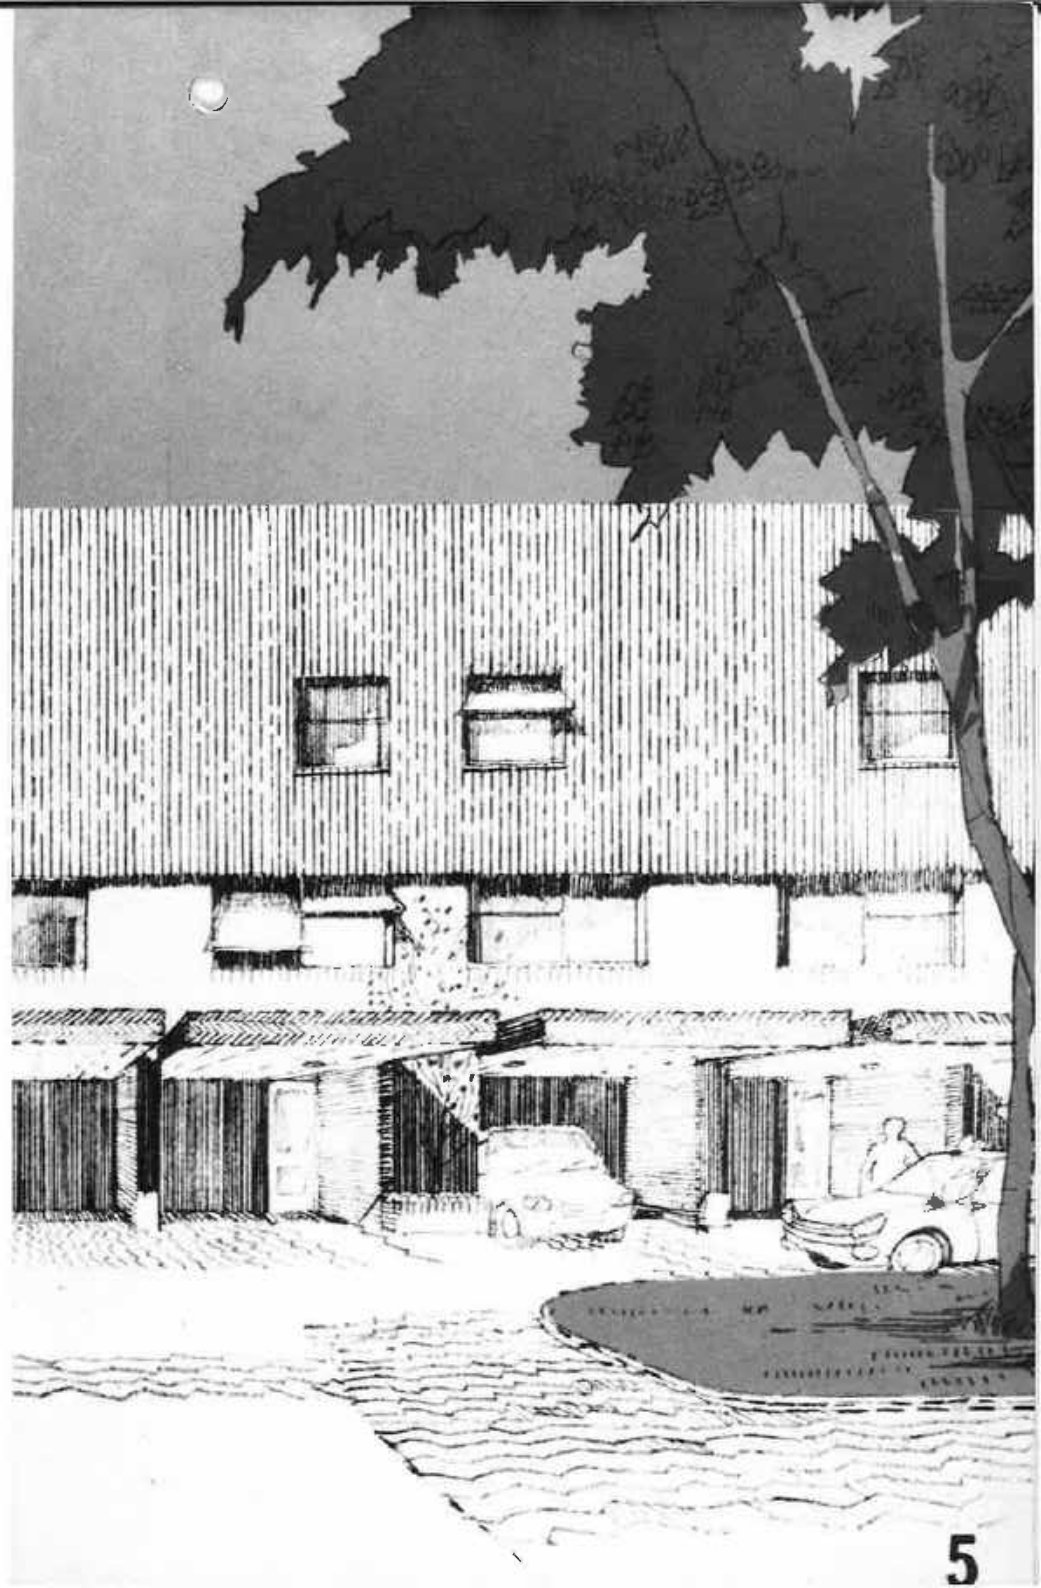

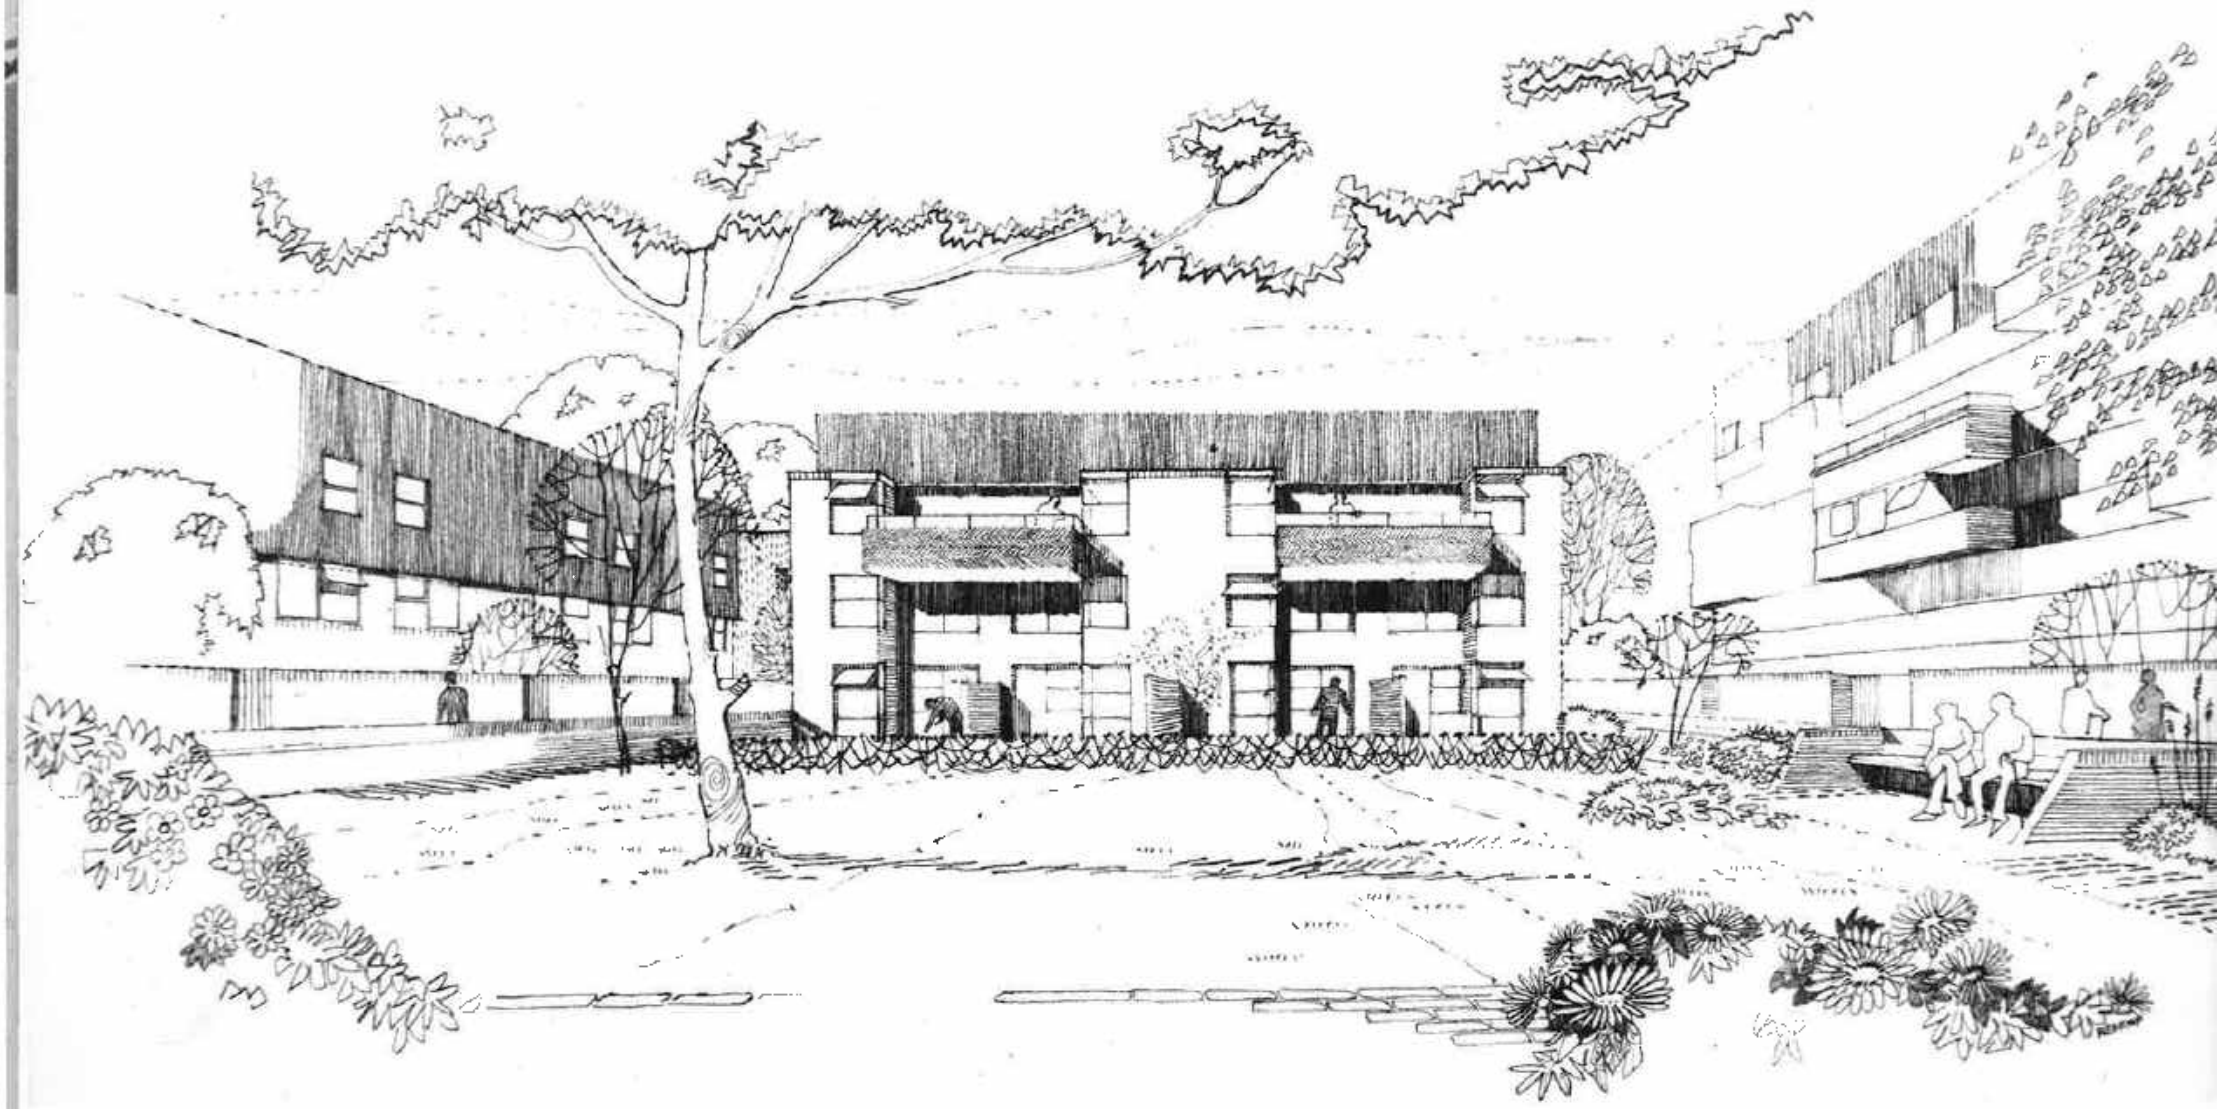

OLD PERSONS FLATS AND
GARDEN

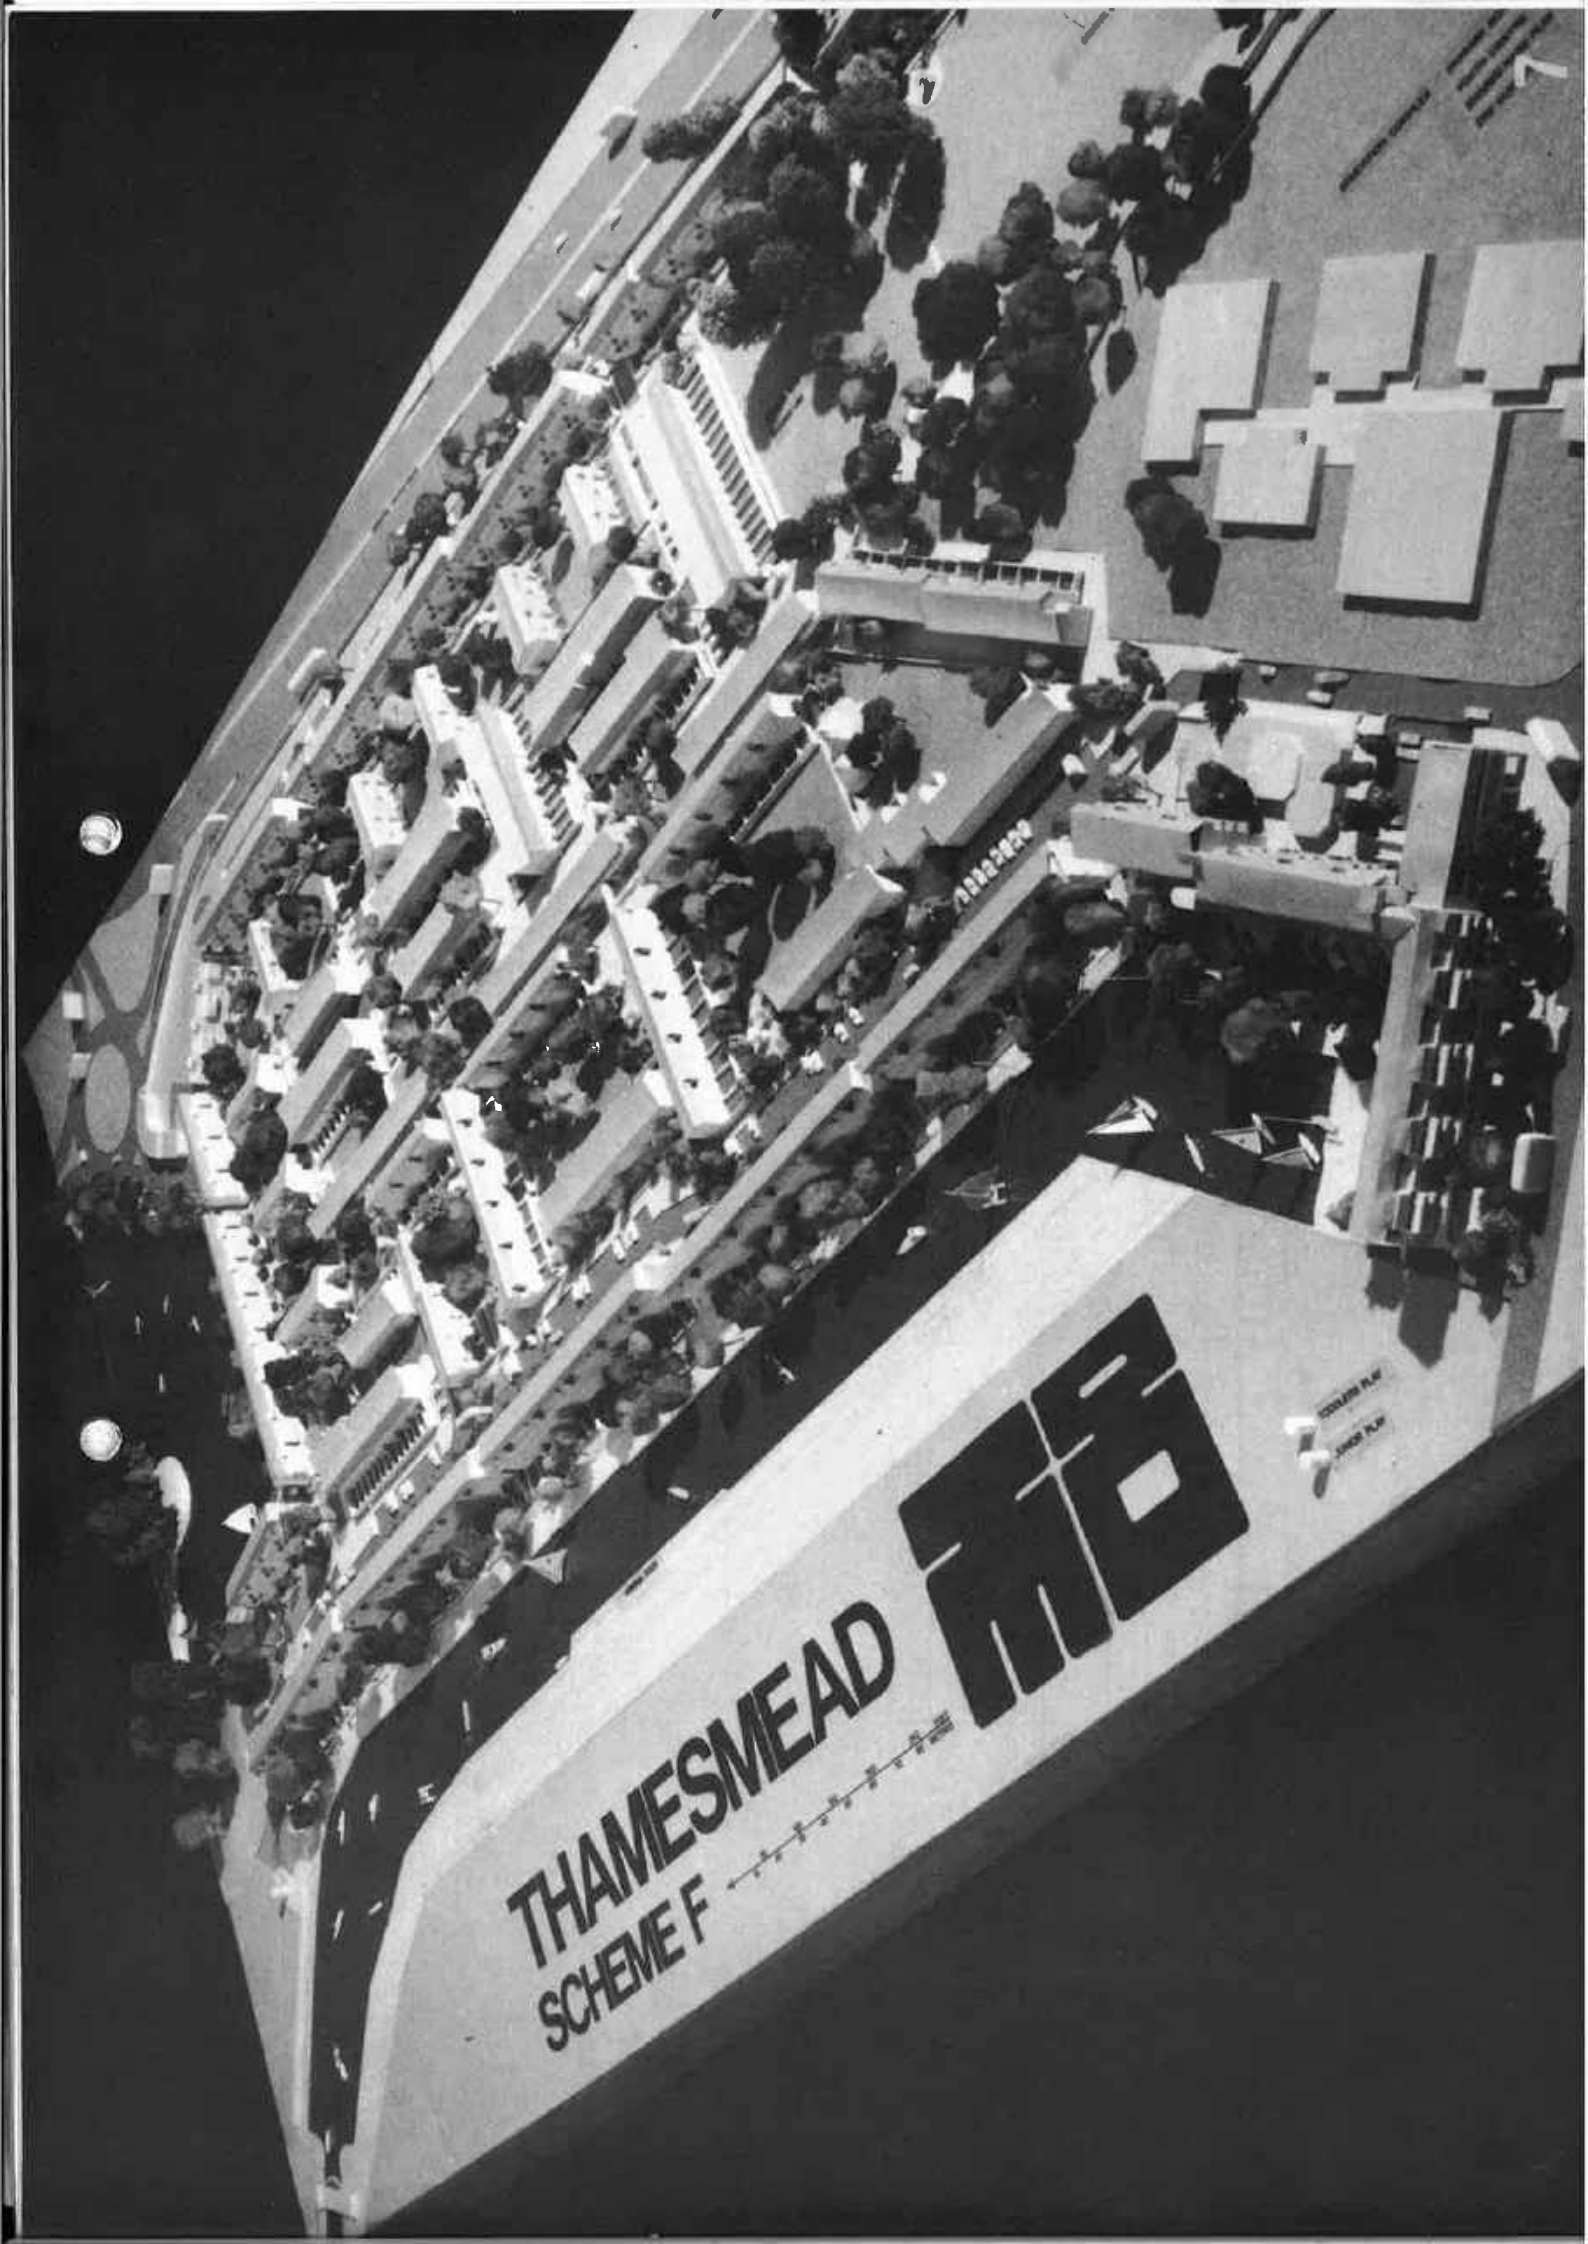
THAMESMEAD
SCHEME F



<1 to <10 indicate viewpoints for elevations on pages 10 and 11.

AREA IVG
layout

AREA IVG

Area IVG is located west of the existing Road 3 and south of the proposed Central Area. The scheme provides for 96 dwellings of which 68 will be 2 and 3 storey family houses with gardens, and the remainder 2 storey 2 person flats. They will be of timber frame construction on piled foundations, faced externally with brick and tile. The layout has been designed in two main areas, each served by a cul-de-sac, separate access to both being from the existing local distributor (Road 3). The existing trees on this site will be retained as a natural feature in the scheme.

Analysis

Gross site area	1.85 hectares (4.57 acres)
Housing area	1.85 hectares (4.57 acres)
Population	386
Density	200 persons per hectare (81 ppa)

Storeys	Type	Persons/Dwellings				Totals	
		II	IV	V	VI	Dwellings	Persons
2	Flats	28				28	56
2	Houses (2 beds)		13			13	52
2	Houses (3 beds)		14			14	56
3	Houses			24		24	120
3	Houses				17	17	102
						96	386

Car Provision:
Garages - 24

Parking Spaces - 32 (initial)
72 (ultimate)


Casual Parking - 6 (initial) 10 (ultimate)
Total 62 (initial) 106 (ultimate)
This is 64% of all dwellings (initial) 110% (ultimate)


Individual gas fired boilers will serve the dwellings with heating radiators and hot water.

A local park of 9 hectares (22.5 acres) will be provided within a short distance of Area IVG, to the south of Area IIIB and adjacent to Lake 2. A wide range of activities are being catered for including playing fields, play spaces and sailing facilities.


It is anticipated that future residents will initially use the shopping and other facilities in the Local Centre in Area III, health services being supplemented for this and other areas by the provision of a temporary Health Centre in Area IIIB.

Primary Schools Nos. 1, 2 and 4 will all be located within a quarter mile distance of the site using pedestrian routes, and will be capable of absorbing the additional intake of pupils from this Area. The secondary school is adjacent to Area IVG and access to it is via the pedestrian route to the north of the site.

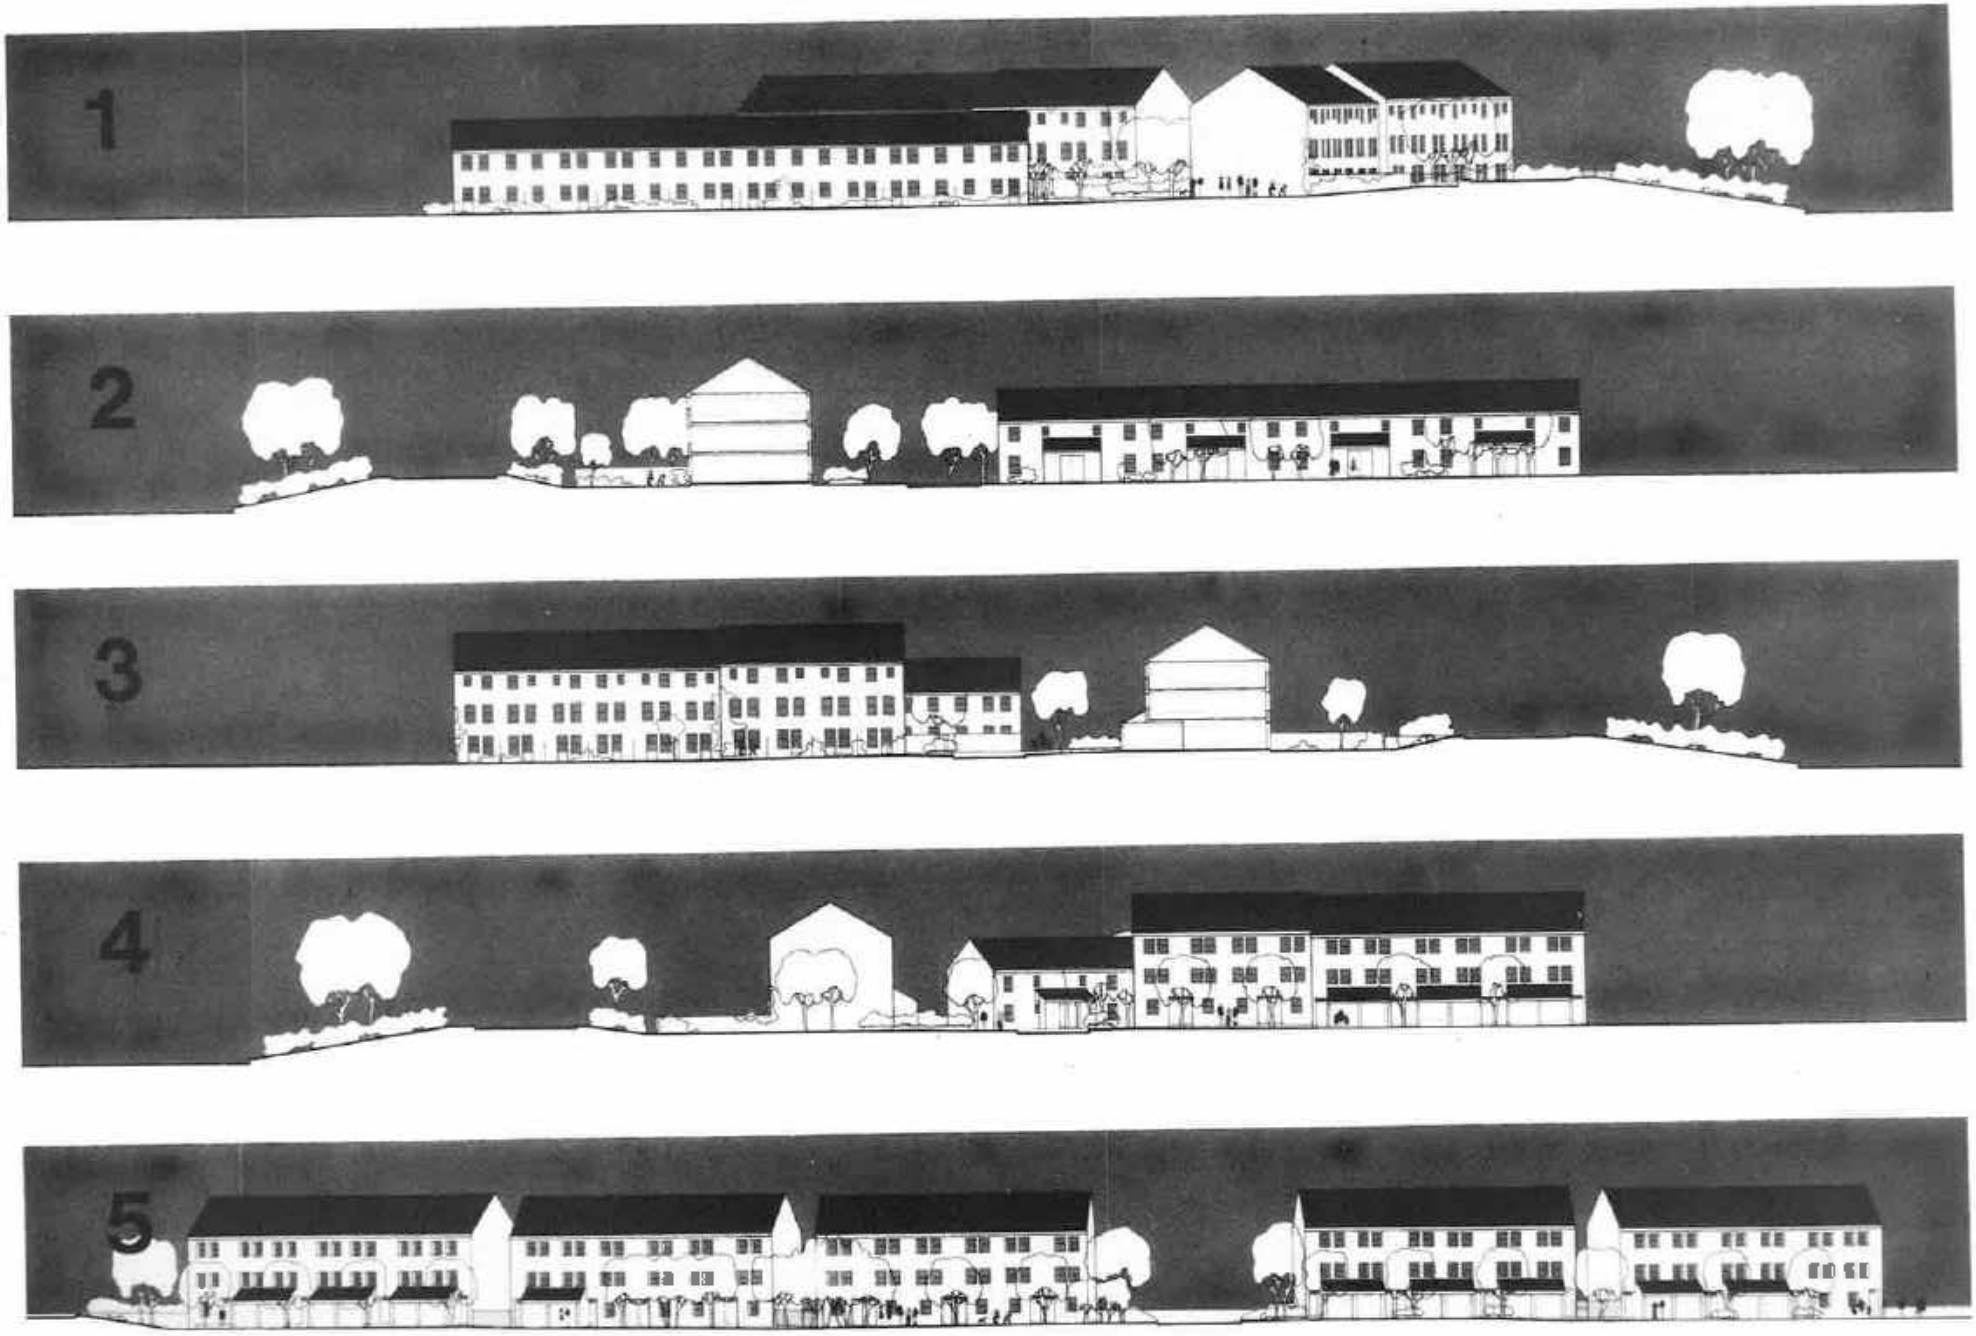
1
2
3
4
5

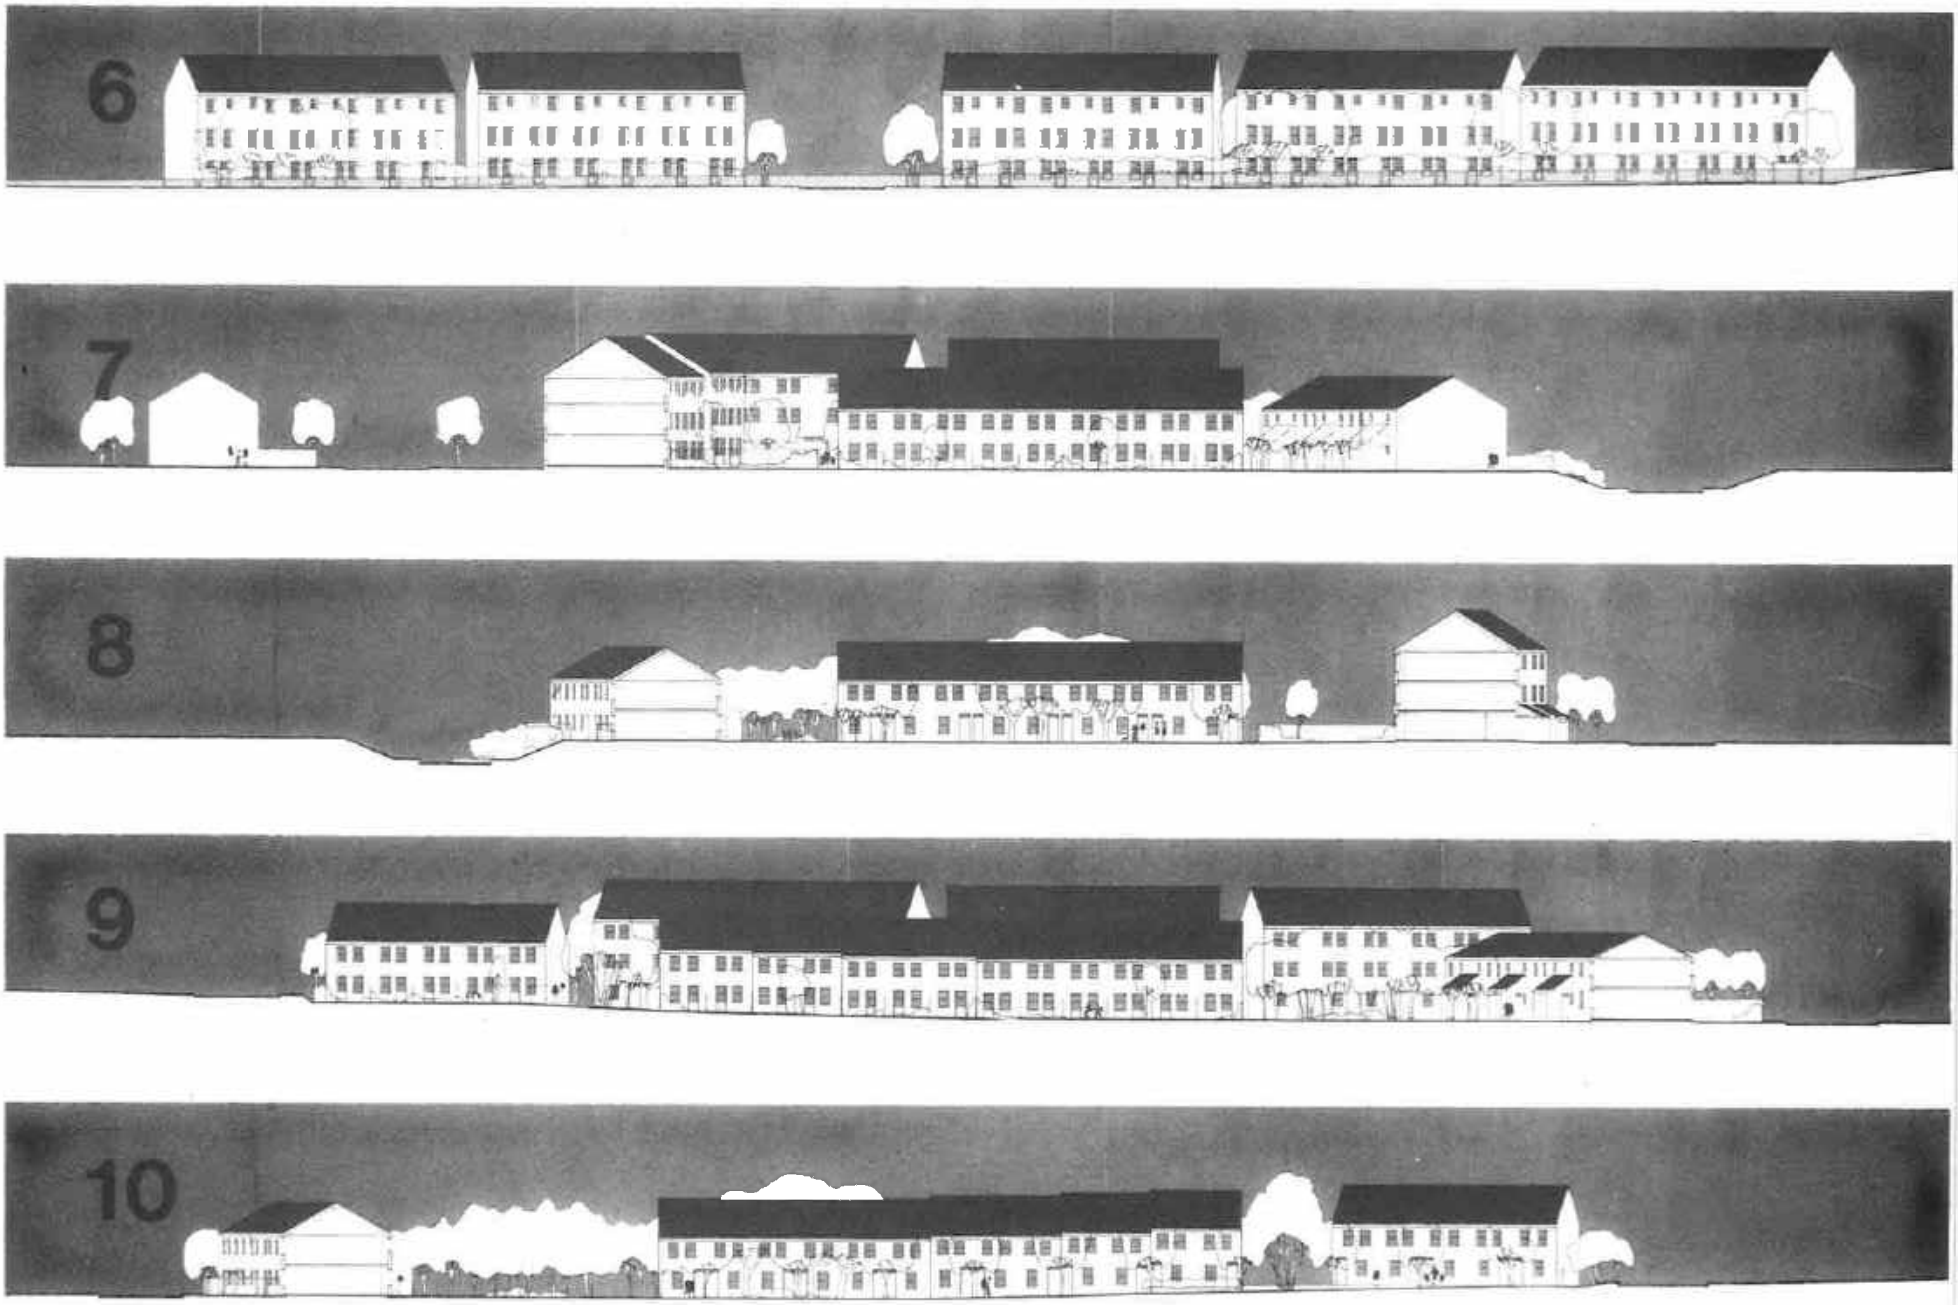
6
7
8
9
10

AREA IIIH layout

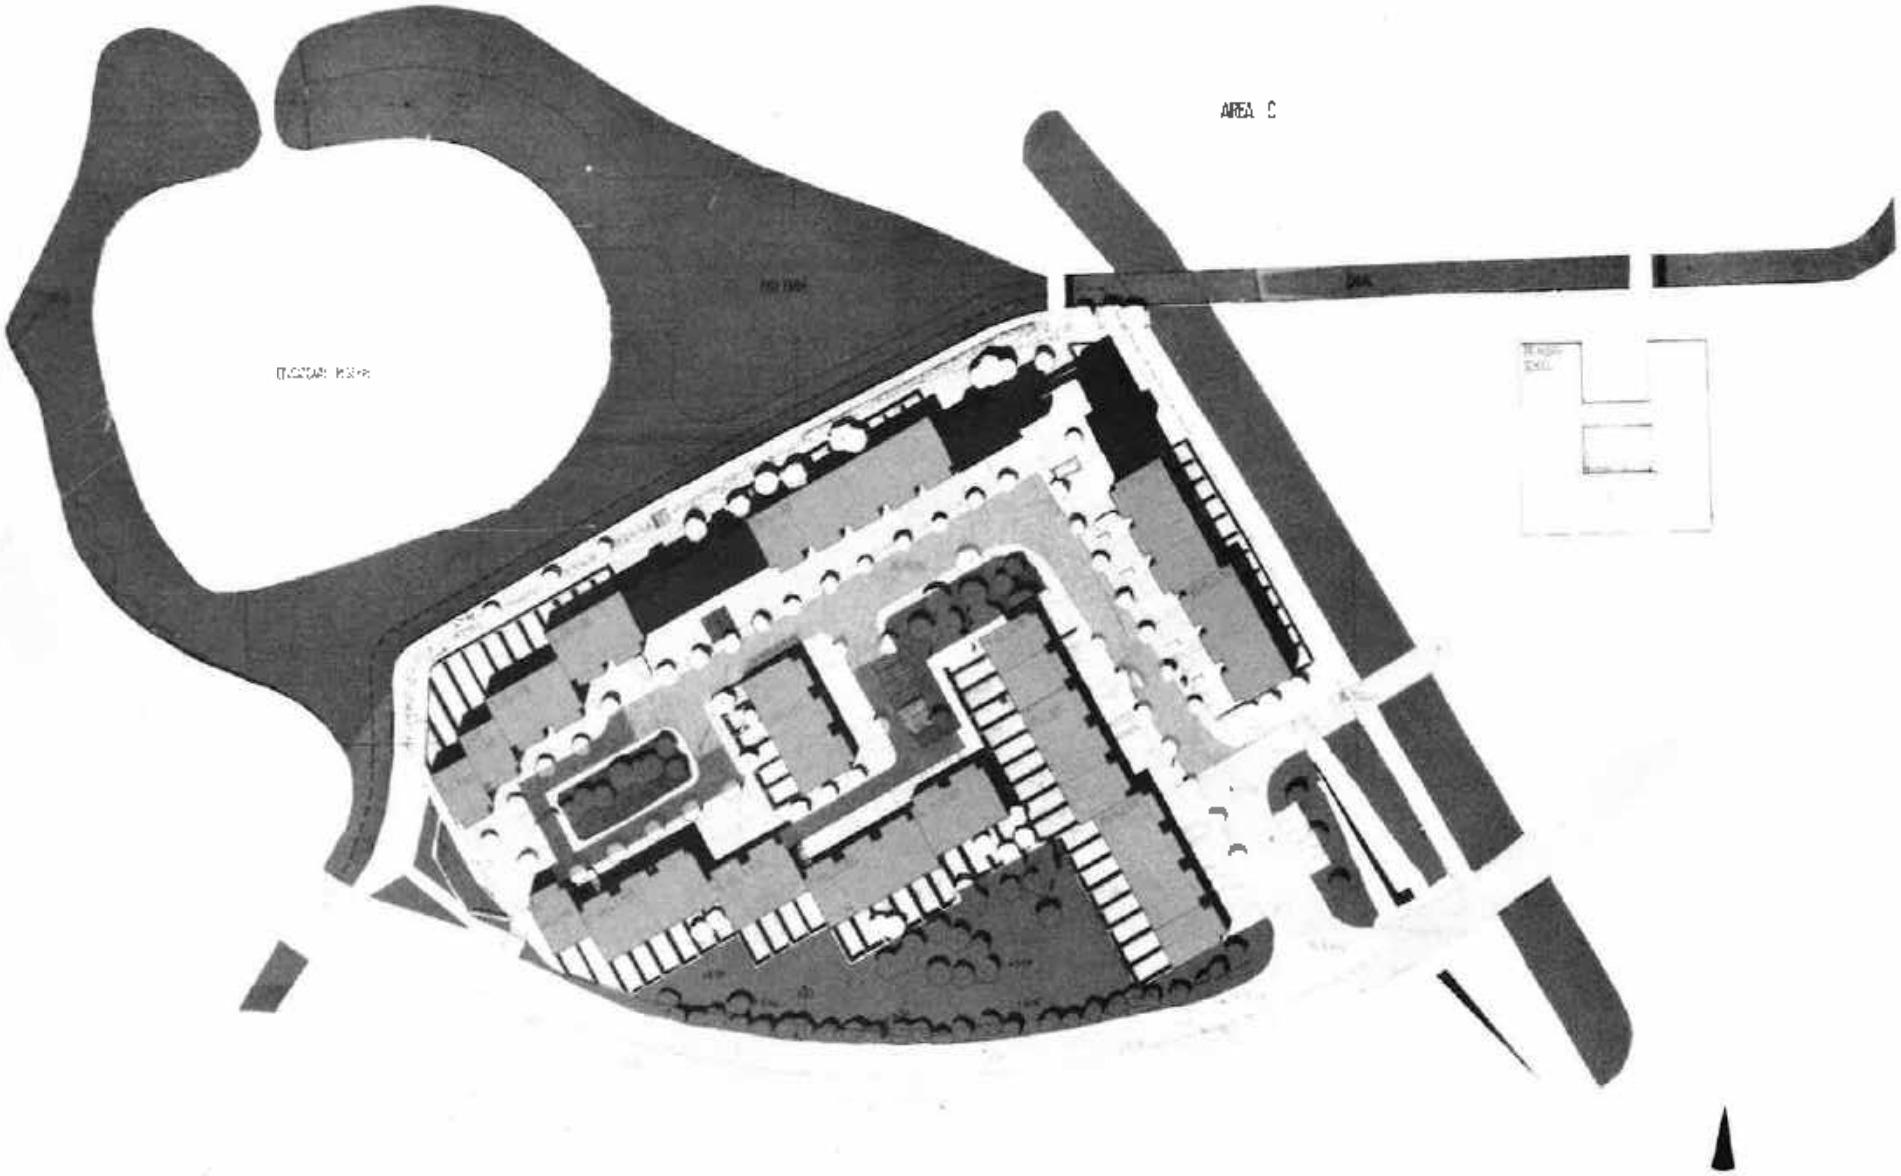

AREAS IIIB and IIIH

Area IIIB is situated south of area IIIH and is separated from it by a distributor road. There will be 98 3-storey 5-person houses with integral garages and gardens, 48 2-storey 4-person houses and 38 2-person flats.

Analysis

Gross site area	4.7 hectares (11.64 acres)
Housing area	3.4 hectares (8.42 acres)
Population	758
Density	222 persons per hectare (90 ppa)

Car provision:
Garages - 120 Parking spaces - 72
Total provision for 192 vehicles, which represents 104% of all dwellings.

Area IIIH is situated west of the Local Centre in Area III. The accommodation will consist of 80 5-person houses with integral garages and gardens, and 21 2-person flats.

Analysis

Gross site area	1.87 hectares (4.63 acres)
Housing area	1.31 hectares (3.20 acres)
Population	442
Density	233 persons per hectare (95 ppa)

Car Provision:
Garages - 96 Parking spaces - 16
Total provision for 112 vehicles, which represents 111% of all dwellings.

All the dwellings in Areas IIIB and H will be traditionally constructed in brick, the 5-person houses having tile hung facades.

Heating and hot water will be provided by individual gas-fired boilers serving hot water radiators throughout the dwellings enabling each to be capable of private ownership.

A 2-form entry Roman Catholic primary school (No. 4) will be established in Area IIIB. Children of primary school age will also be able to attend Windrush School (east of Area IIIH) and the 2-form entry primary school No. 2 (west of Area IIID). There is a secondary school in Area IV.


Eventually the Main Health Centre which is programmed for construction near the proposed Central Area will serve this area, but as an interim measure the Greenwich and Bexley Area Health Authority are providing a temporary health centre in Area IIIB.

Storeys	Type	Persons/Dwellings			Totals	
		II	IV	V	Dwellings	Persons
Area IIIB						
3	Flats	38			38	76
3	Houses			98	98	490
2	Houses		48		48	192
Area IIIH						
3	Houses			80	80	400
3	Flats	21			21	42
					285	1200



AREA IIIB layout



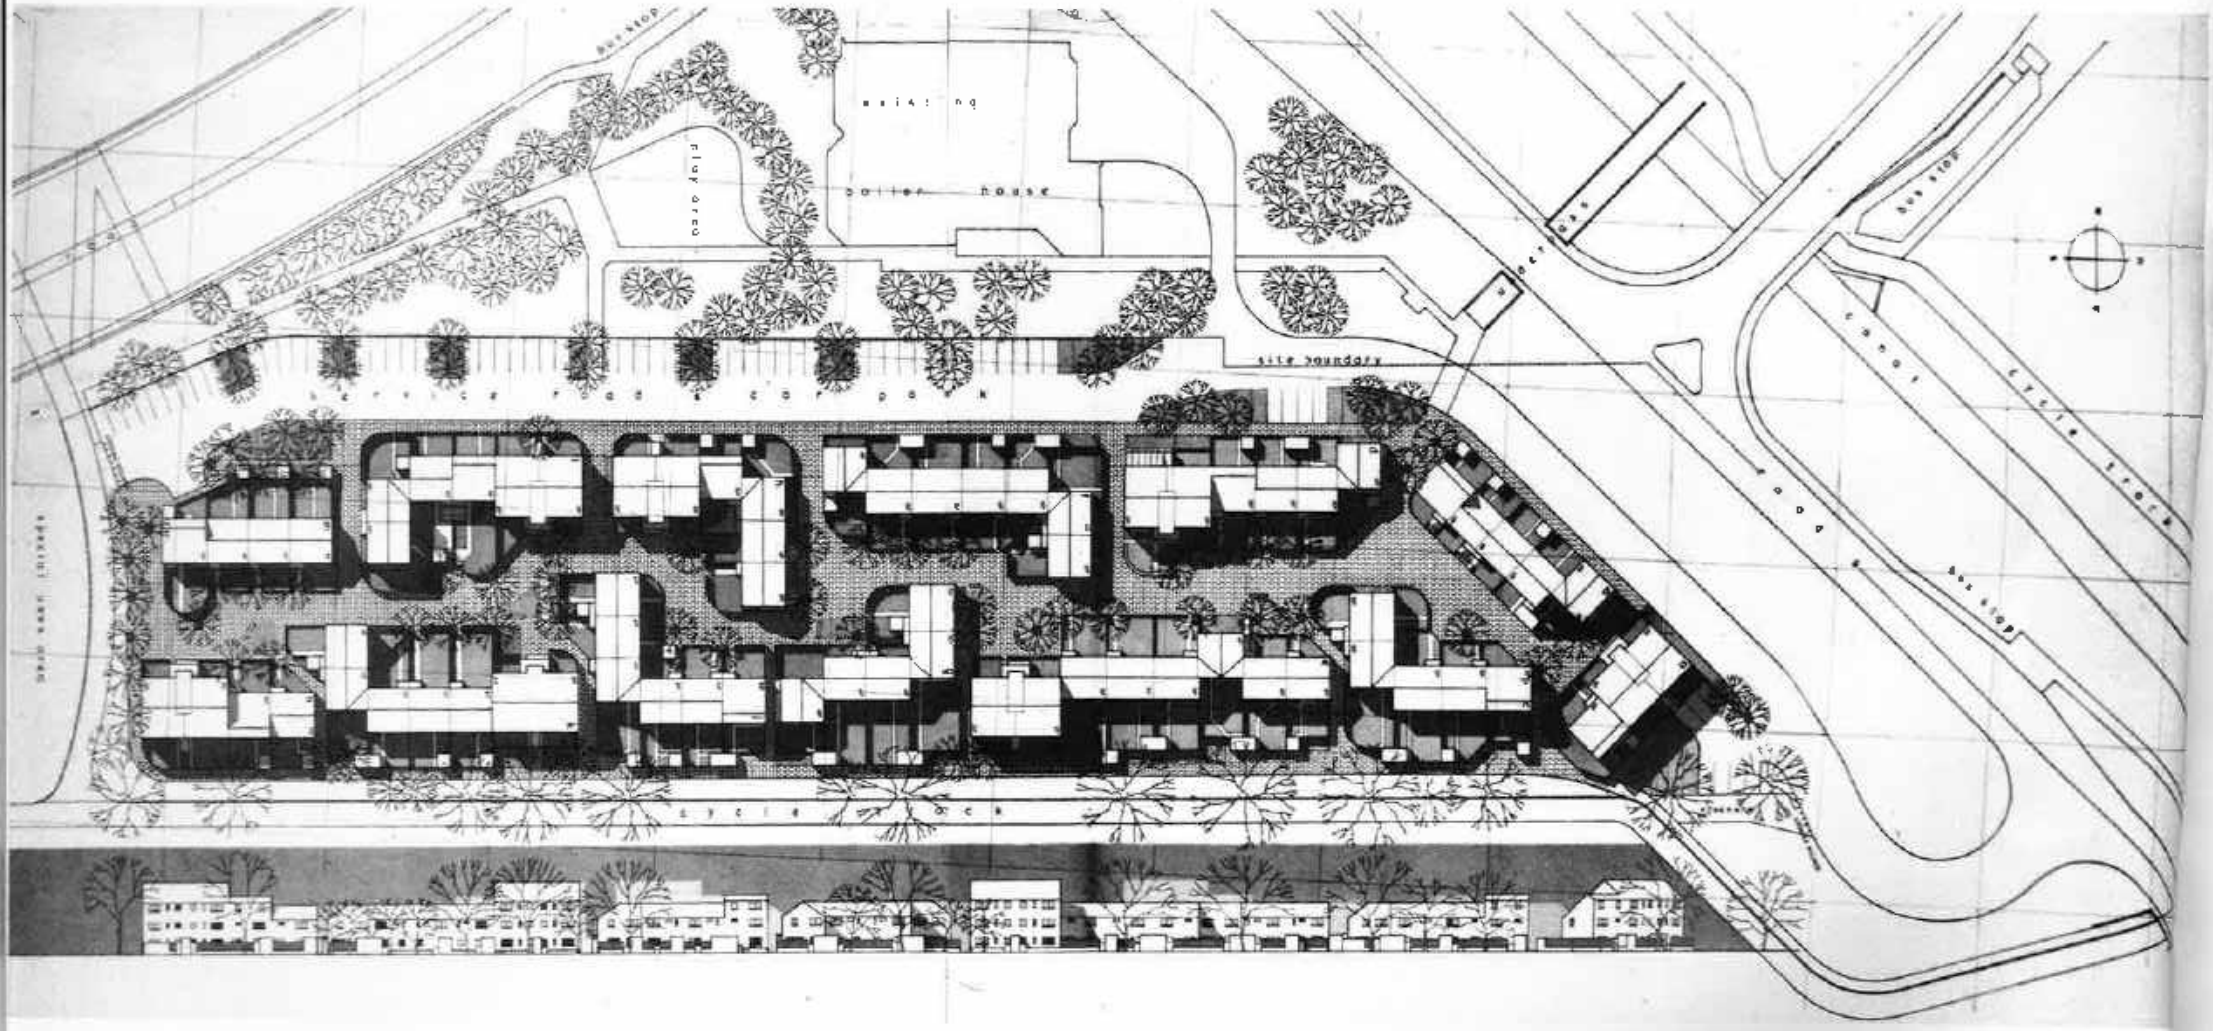

thamesmead area 3L



thamesmead area 3L

AREA IIIL

This development lies to the east of Area III Local Centre, and will provide 99 traditionally constructed dwellings of low/medium rise.

The dwellings will be grouped parallel to the former Harrow Manorway (the boundary between the London Boroughs of Bexley and Greenwich), and the valuable row of black poplars along this boundary will be retained. The proposal is for the development to be basically traffic free with all vehicles being confined to an access/ service road. Emergency vehicles will be the exception.

Car parking will be along the access road only, 60 parking spaces being provided for immediate use with 30 for future use.

Analysis

Gross site area	1.9 hectares (4.7 acres)
Housing area	1.54 hectares (3.8 acres)
Population	347
Density	182 persons per hectare (75 ppa)

Storeys	Type	Persons/Dwellings					Totals	
		OP II	II	IV	V	VI	Dwellings	Persons
3	Flats	27	14				41	82
2	Houses			34			34	136
2	Houses				15		15	75
2/3	Houses					9	9	54
							99	347


Each family dwelling will have a garden, and therefore no play spaces will be provided within the housing area. Play and leisure activities can be pursued in the nearby public open space at the southern end of the site.

A small development such as this would normally be regarded as unsuitable for district heating, but with the boiler house immediately adjacent it is economic for these dwellings to be served from the heating main, rather than from individual boilers.

A subway to the north-west will provide a good pedestrian route to the Area III Local Centre, and therefore an old people's common room will be the only ancillary building provided.

The majority of children from Area IIIL are likely to attend Primary School No. 5 to the north-west when it is completed, but Primary Schools Nos. 1, 2 and 4 will serve the development as an interim measure.


The building and civil engineering work will be carried out under one lump sum contract.

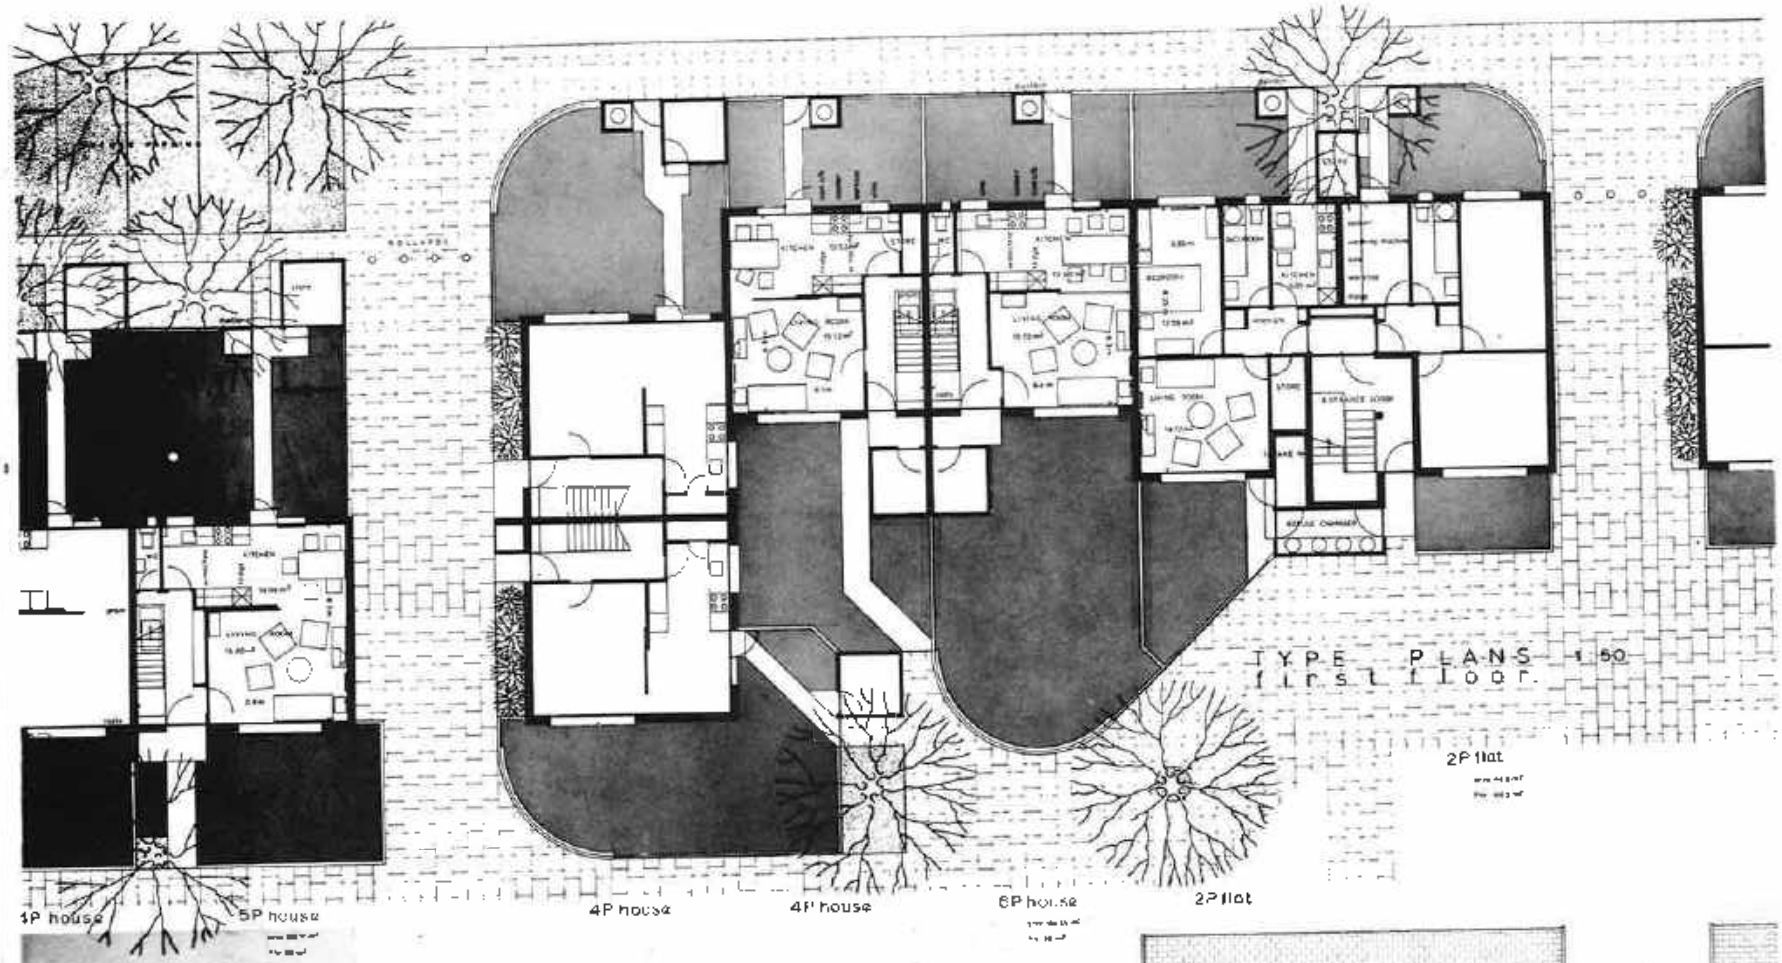


TYPE PLANS 1:50
first floor.




EAST ELEVATION 1:50

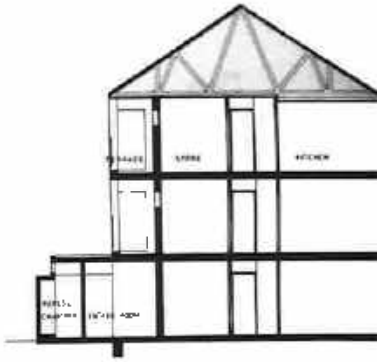

section 2P flats 1:5

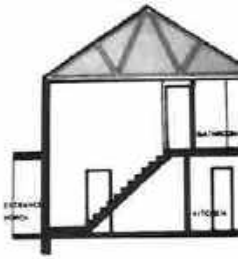

section 4P hous

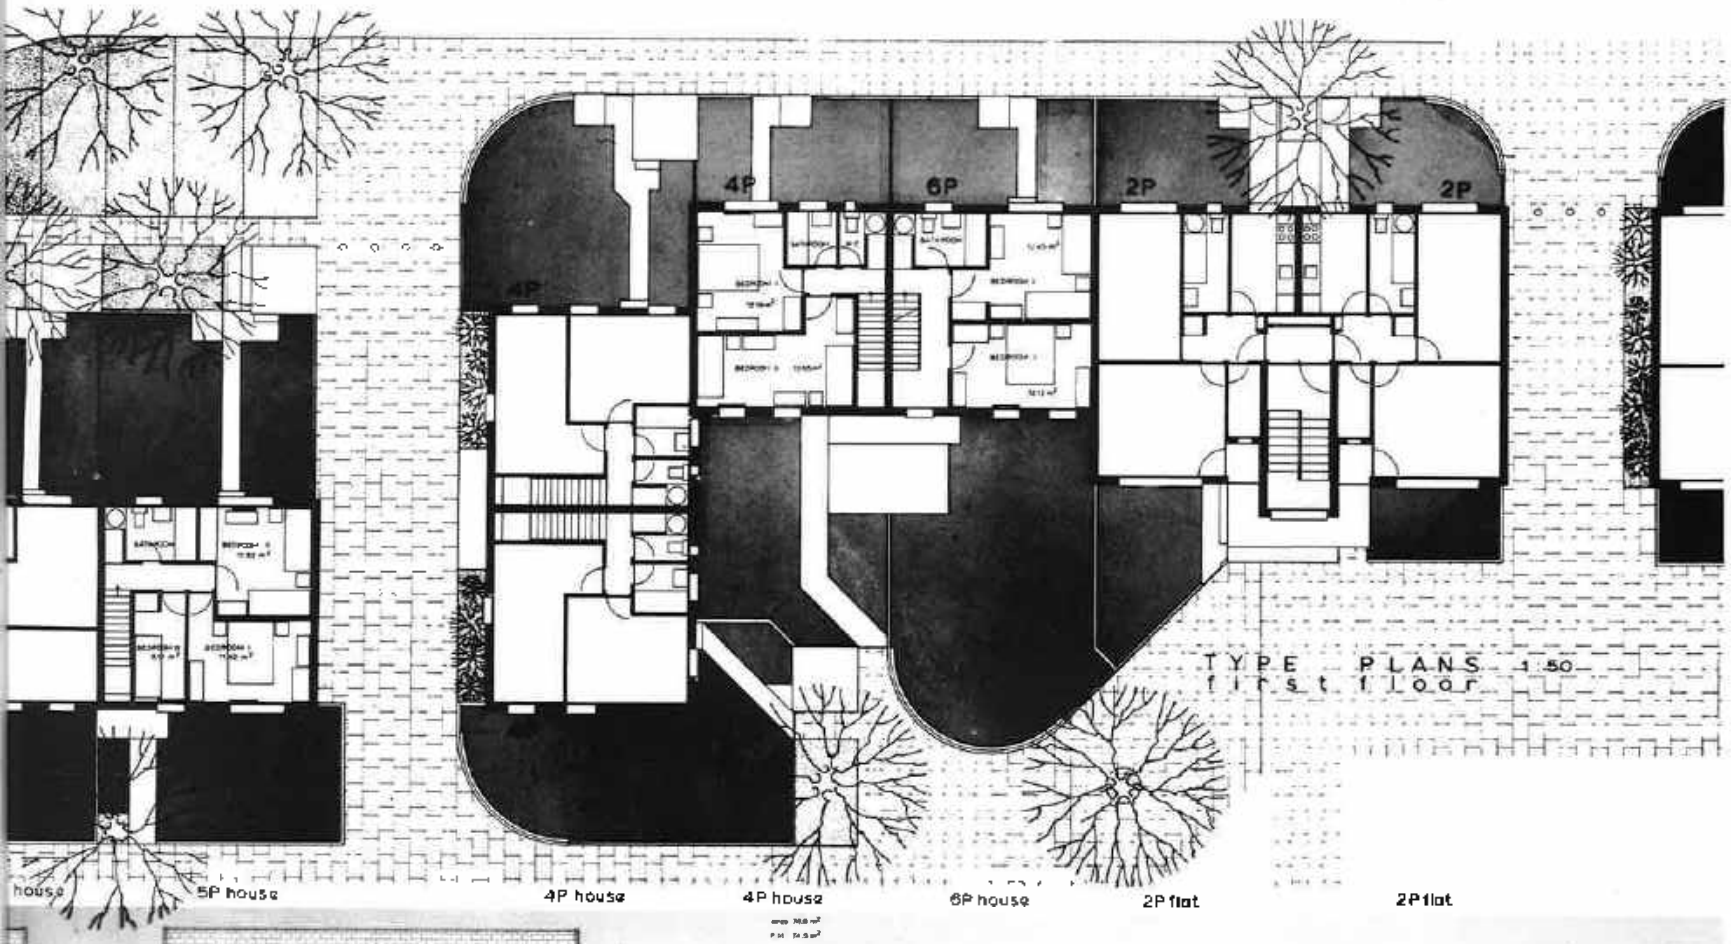




WEST ELEVATION 1:50




section 6P house

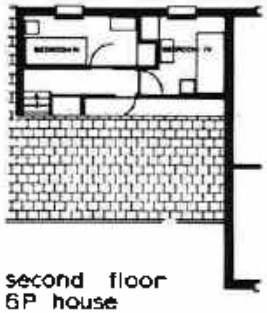

second floor
6P house



section 5P house

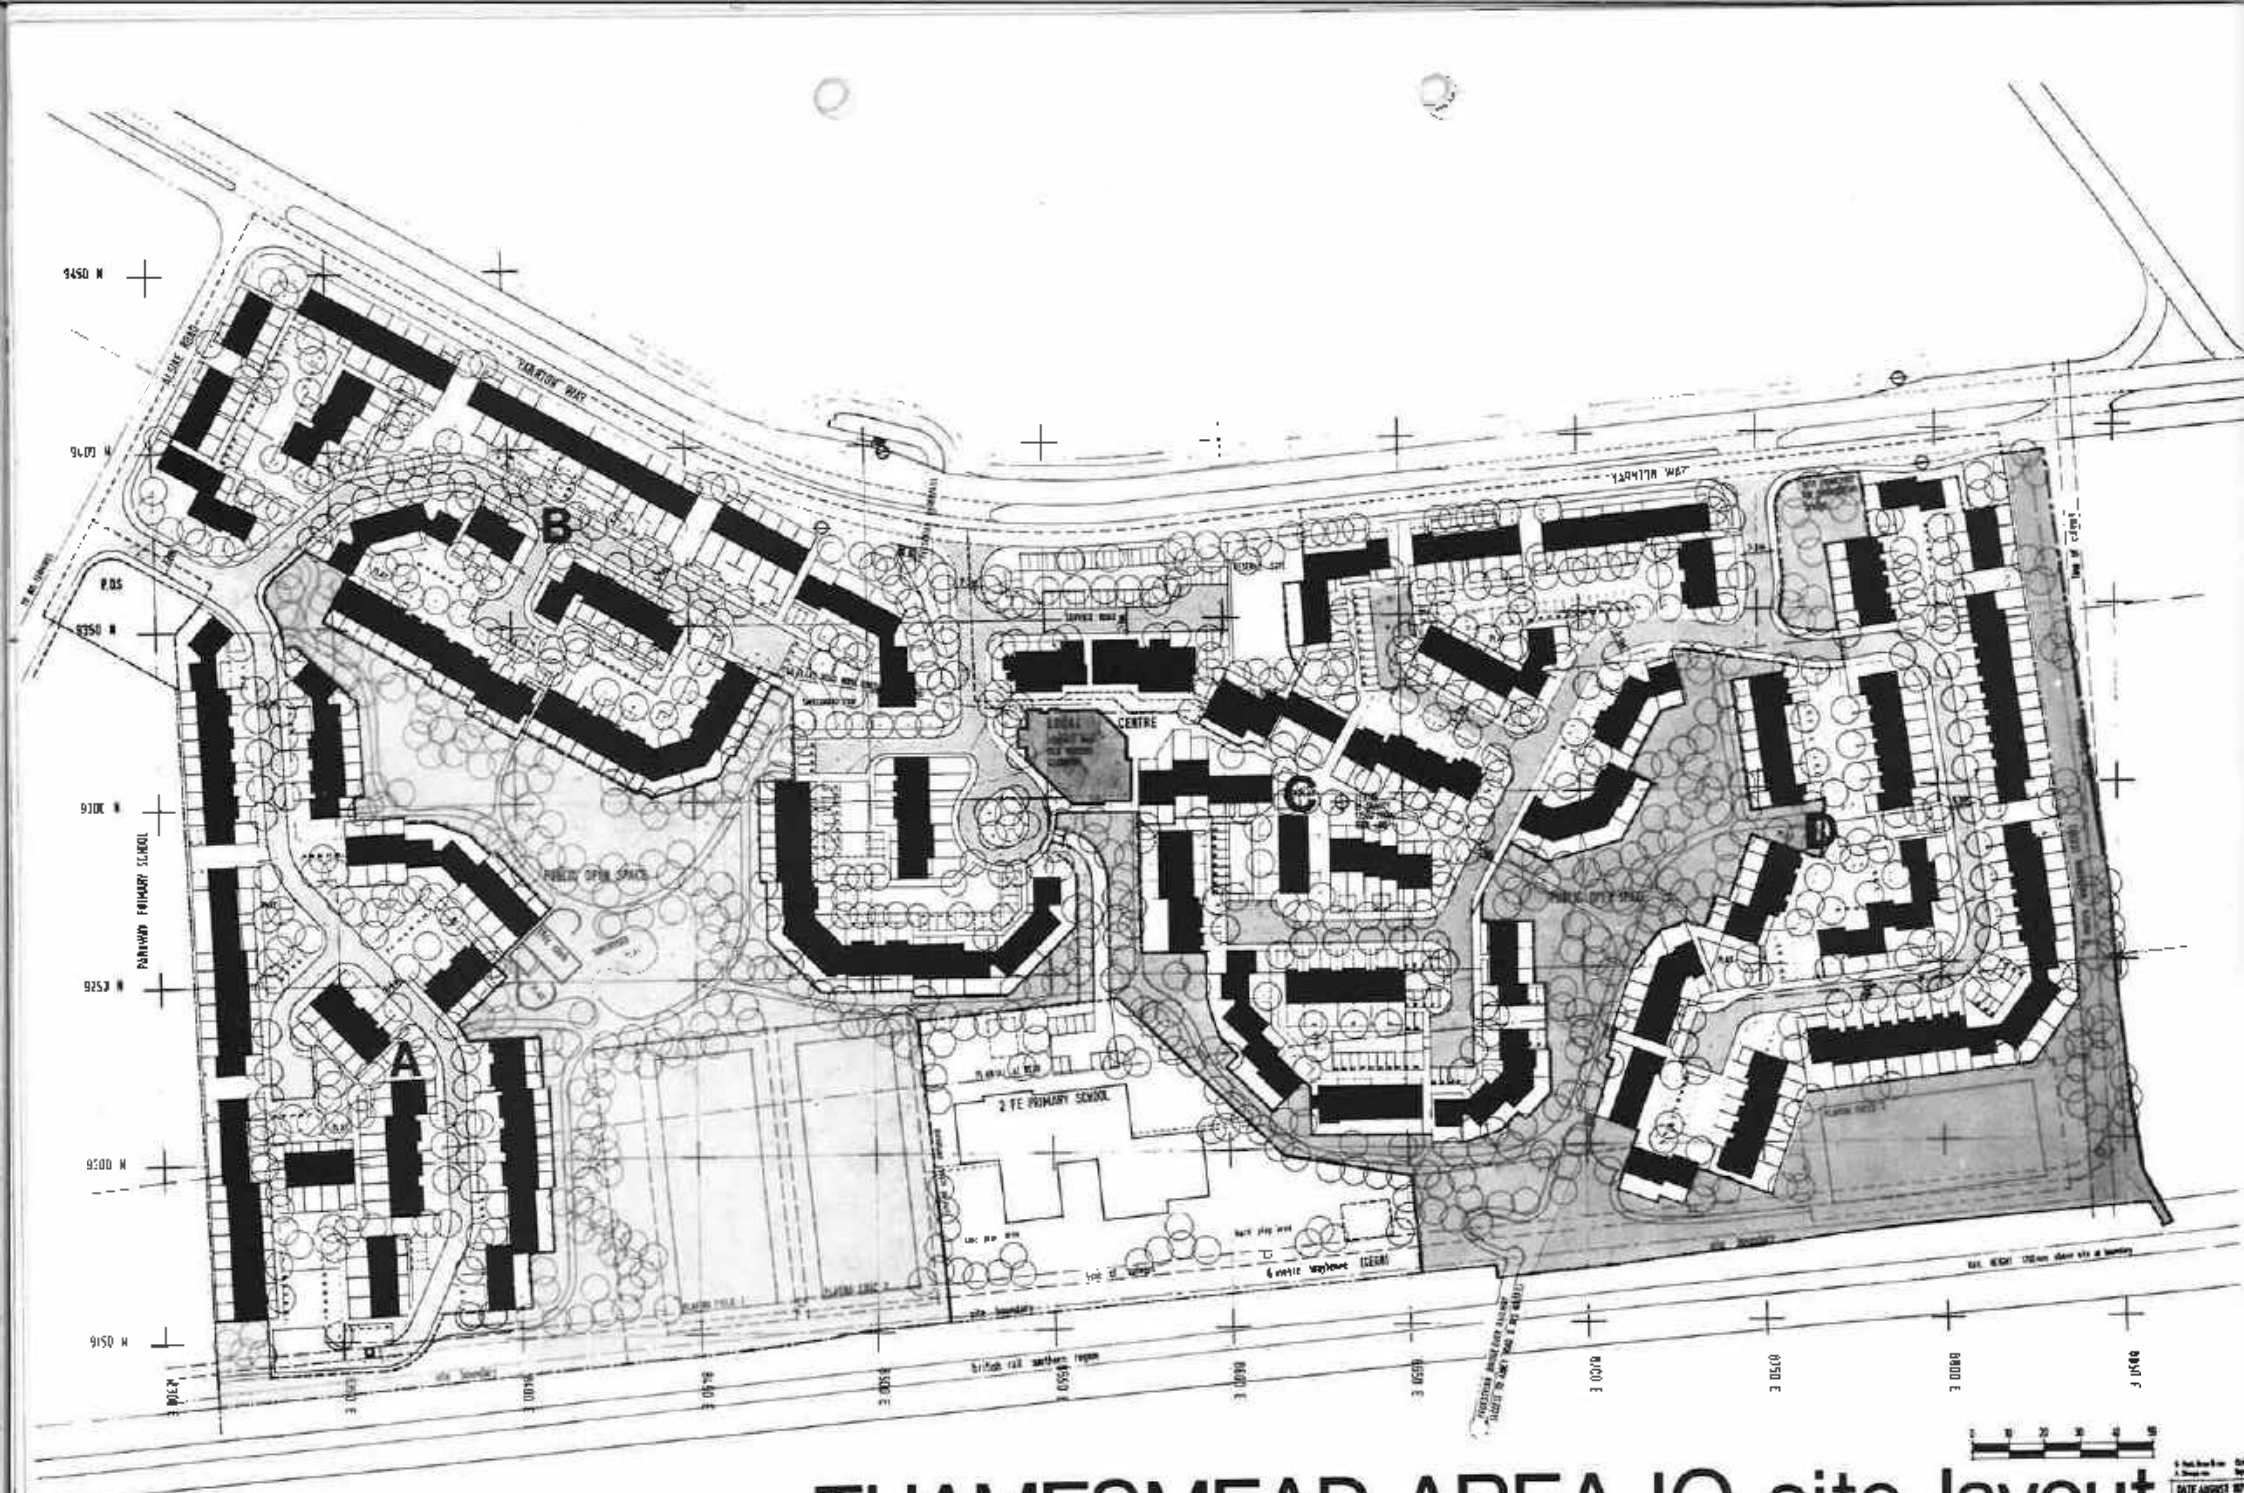
A
B
C
D
PUBLIC OPEN SPACE
2 FE PRIMARY SCHOOL
CENTRE
PUBLIC OPEN SPACE
PUBLIC OPEN SPACE
PARKVIEW PRIMARY SCHOOL
site boundary
site boundary
site boundary

AREA X

This project is located south of Yarnton Way and immediately to the east of Area II. The development is to be low/medium rise, traditionally constructed in brick with tiled roofs. The layout has been designed on the basis of four neighbourhood areas of approximately 140 dwellings each, approached by culs-de-sac and separated by a total of 3.6 hectares (9 acres) of open space forming a local park. The design of the dwellings allows a proportion of them to be sold if required.

Analysis

Gross site area	12.77 hectares (31.56 acres)
Housing area	8.24 hectares (20.37 acres)
Population	1912
Density	232 persons per hectare (94 ppa)
Car Provision:	
Garages - 211	Parking spaces - 200

Facilities are provided for 74% of all dwellings.

Nearly half the dwellings face directly onto the local park and the remainder are all less than a minutes' walk away. All family units have a garden of their own, and major services are concentrated on the party wall in order that the position of the partitions can be altered with relative ease should it be required at a later date. The 3 storey blocks of flats are fitted with a porter alarm system in the entrance hall, which ensures security and privacy. The houses have individual gas fired boilers.

Old persons' dwellings are located in the lower two floors of the 3 storey flats. There is group heating to these units.

The Local Centre is at the heart of the scheme and will provide seven shop units, four of which will be combined to form a small supermarket. Three additional units will be reserved for future shopping provision and used for community facilities at the outset. The clubroom is designed for old people and tenants' use and it will also be used by residents on the neighbouring Area IX. It will have a separate bar and lounge.

A pedestrian bridge across the railway will provide access to bus services on Abbey Road to the south, and a subway under Yarnton Way will provide a route to Riverside Secondary School.

A two form entry primary school will be provided. It will have four acres of playing fields which extend the five acre local park to nine acres of effective open space through their shared use. The playing fields are unfenced and will have three pitches that will be available to residents outside school hours.

A site has been reserved to the north of the local centre for future community use.

Tenders will be invited for the advance civil engineering contract on a competitive lump sum basis. Since the site has been designed on the basis of four neighbourhood areas this lends itself to letting four individual lump sum building contracts.

Storeys/ Type	Persons/Dwellings							Totals	
	OP II	II	IV	V	VI	VII	VIII	Dwellings	Persons
3 2P Flats	152	96						248	496
2 4A Houses			80					80	320
2 4B Houses			50					50	200
3 4C Houses			25					25	100
3 5P Houses				128				128	640
2 6 Houses					6			6	36
3 7P Houses						8		8	56
3 8 Houses							8	8	64
								553	1912




street elevation of 8p 7p 5p 4a & 6p houses + section thro' 7p ● area 10b



rear elevation ● area 10b

typical elevations


THAMESMEAD AREA 10
DATE SEPTEMBER '75
SCALE 1/100
DRG NO. 9167/0031

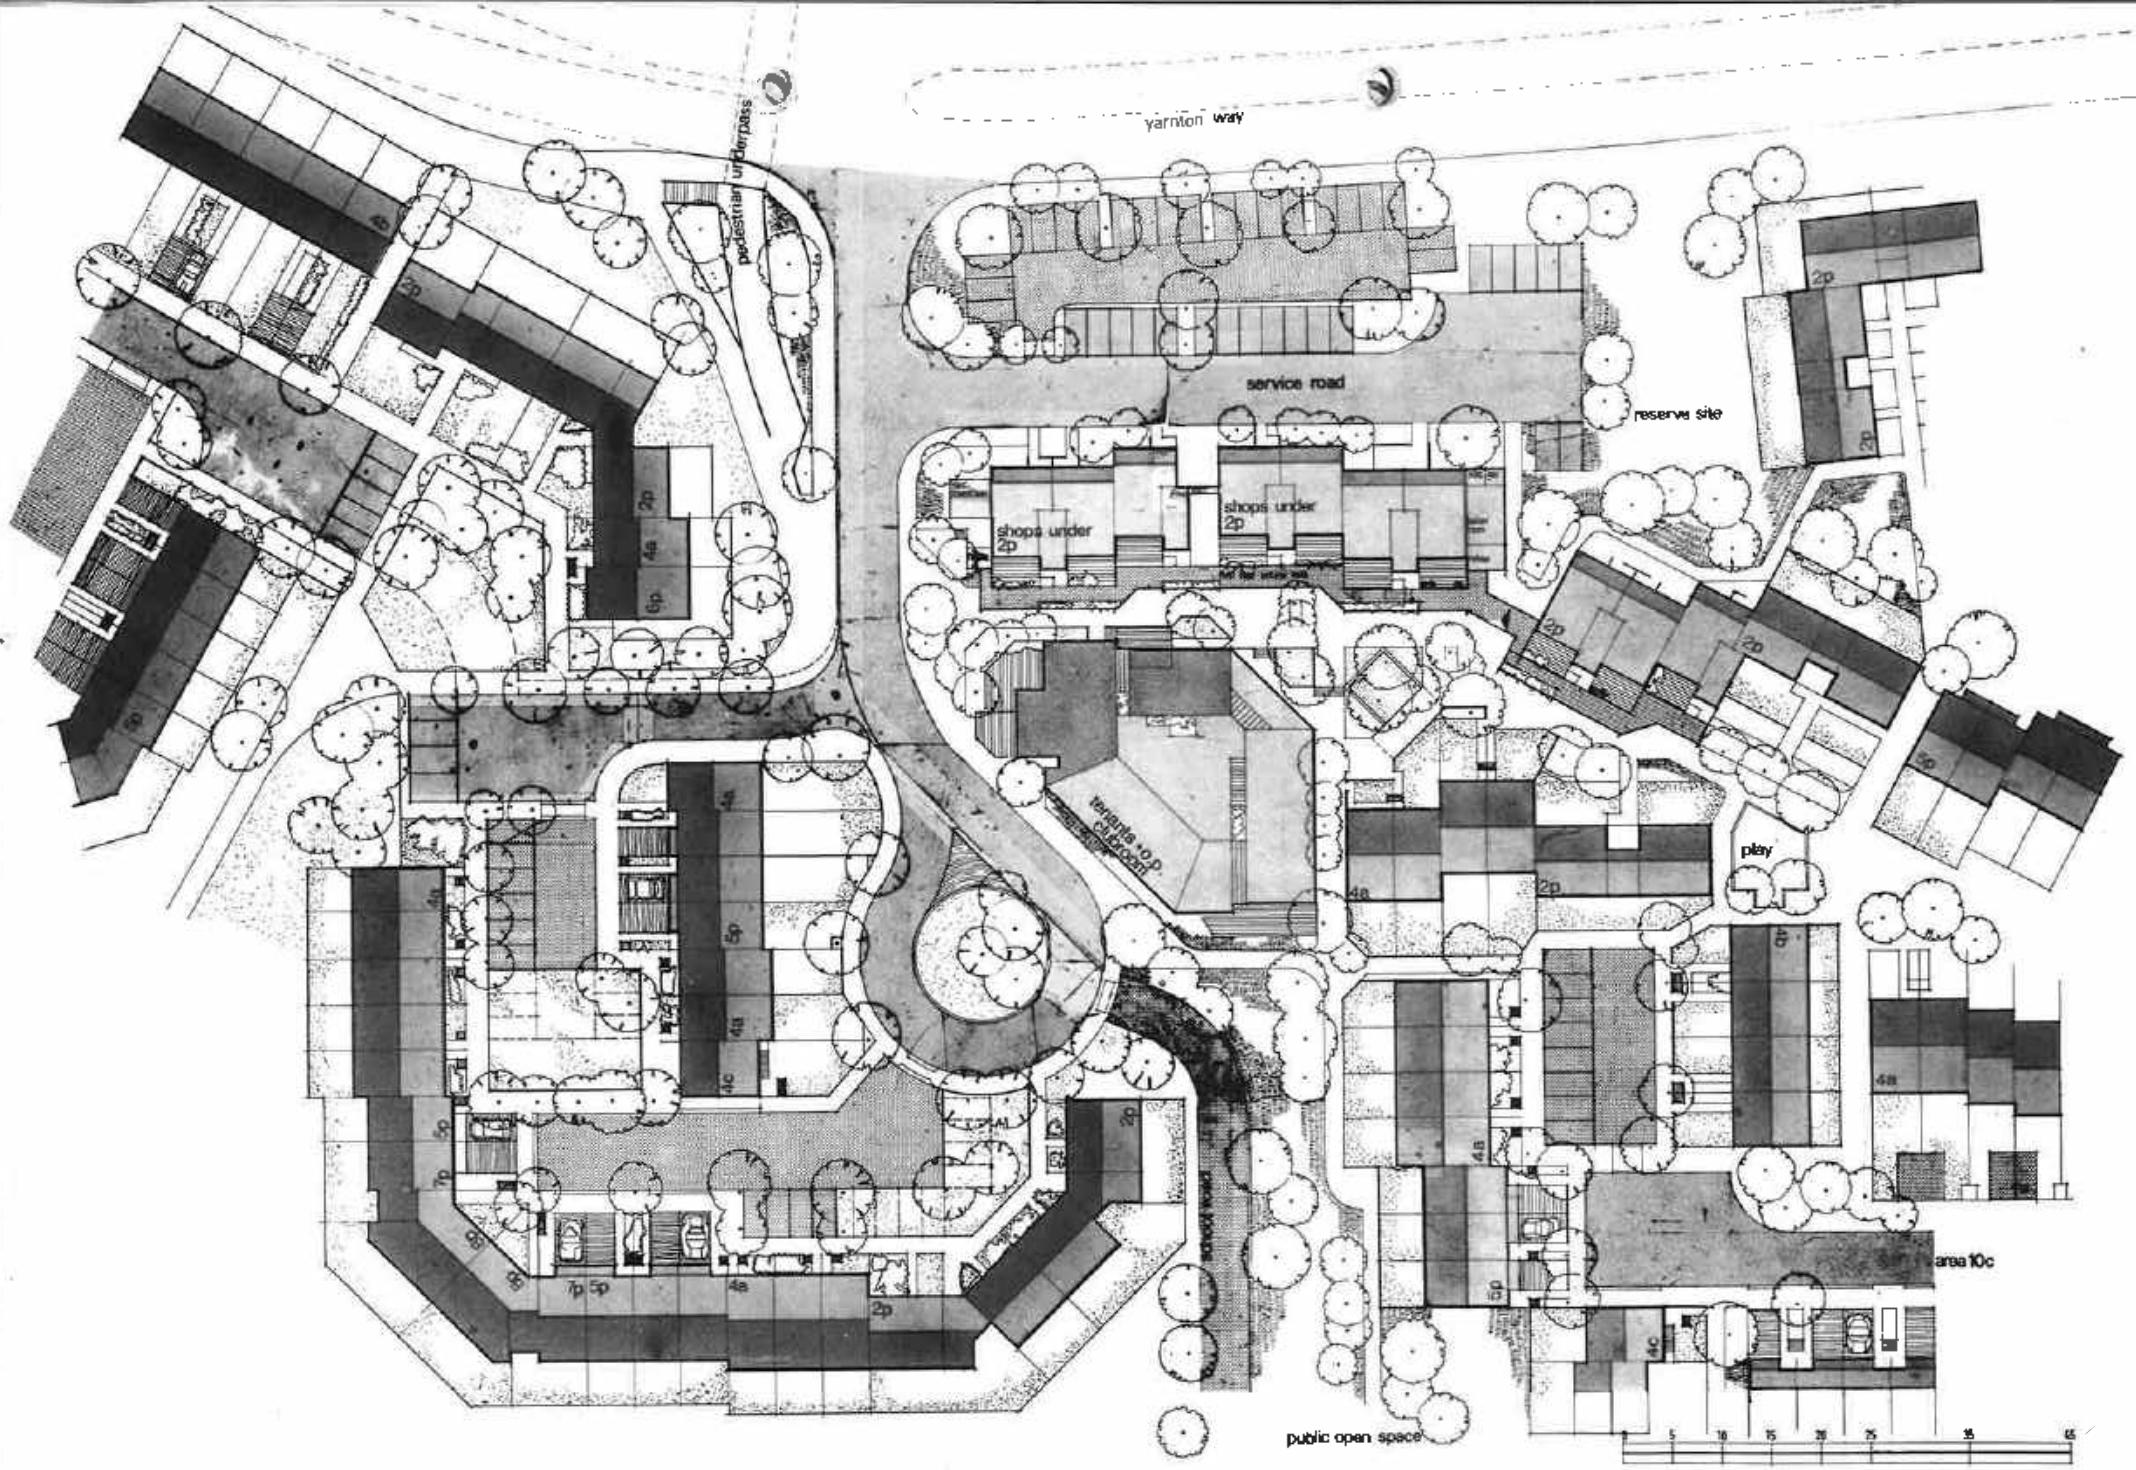

local centre 23



Ground Floor Plan

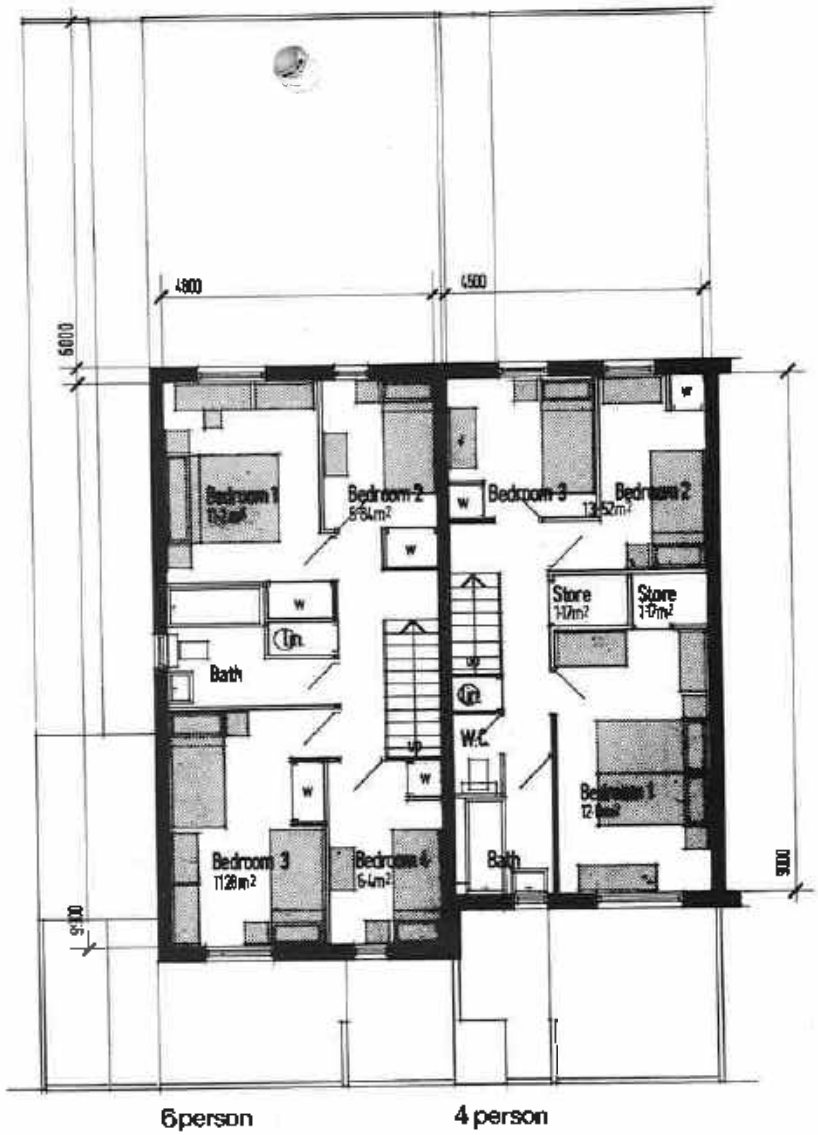

First Floor Plan


Total Areas for 6 person		P.M. Areas
Gross overall	96·20m²	97·0m²
Net space	90·89m²	92·5m²
Storage	4·59m²	4·5m²

Total Areas for 4a		
Gross overall	80·23m²	79·0m²
Net space	75·11m²	74·5m²
Storage	4·42m²	4·5m²

Key wm · washing machine
l · larder f · fridge b · boiler
brms · brooms ccu · elect. meter
—— non-structural partition

0 1 2 3 4 5

4a+6 person houses

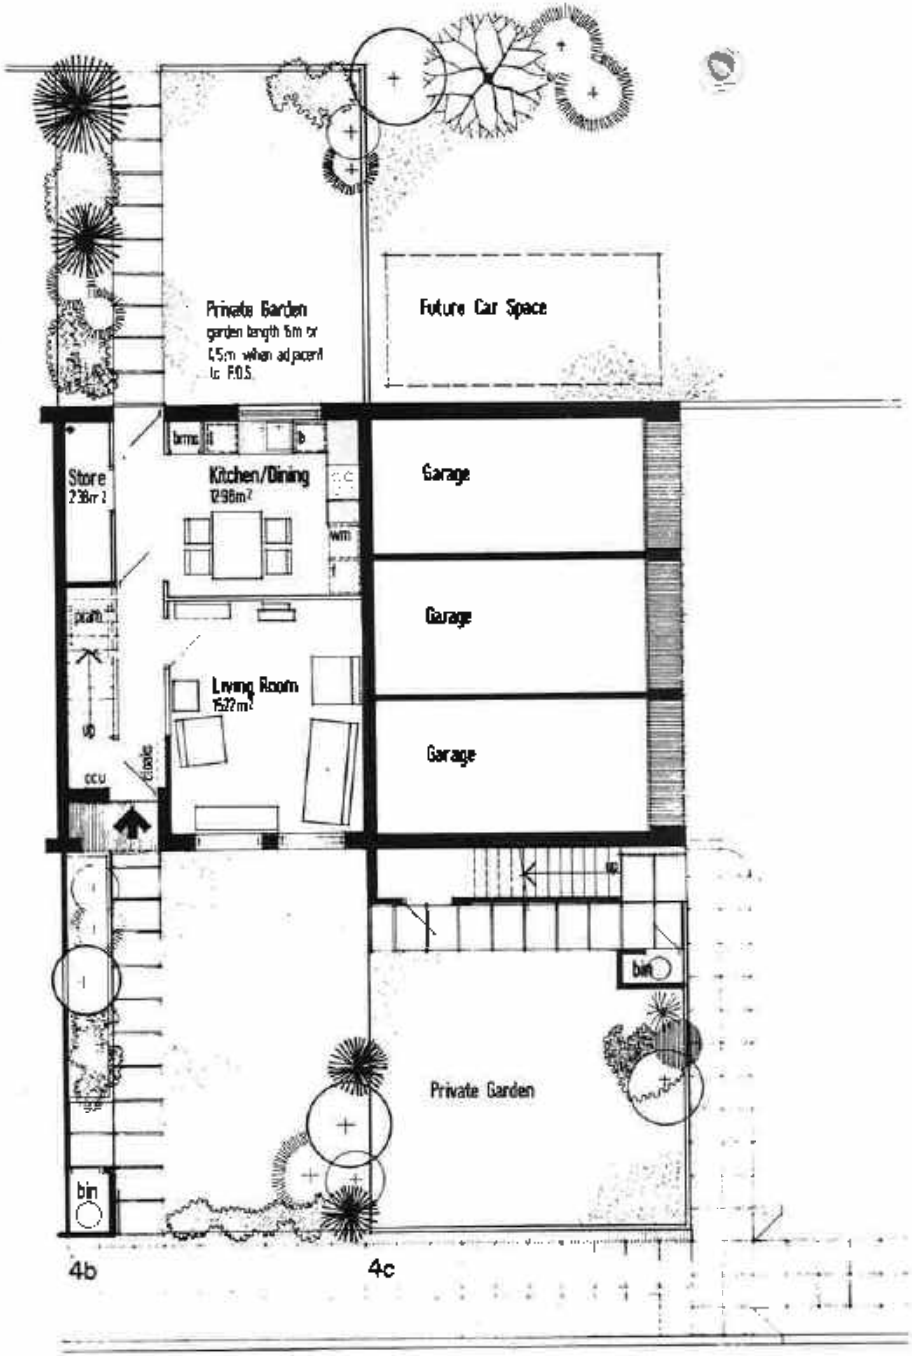

Ground Floor Plan



First Floor Plan 4c



First Floor Plan 4b
Second Floor Plan 4c


0 1 2 3 4 5

Total Areas		P.M. Areas
Gross overall	79.59m²	79.0m²
Net space	74.26m²	74.5m²
Storage	4.61m²	4.5m²

Key wm · washing machine
t · larder f · fridge b · boiler
brms · brooms ccu · elect. meter
—— non-structural partition

4 person houses · b+c

THAMESMEAD AREA 10
DATE AUGUST 1975
SCALE 1:50
DRG NO 9167/0010

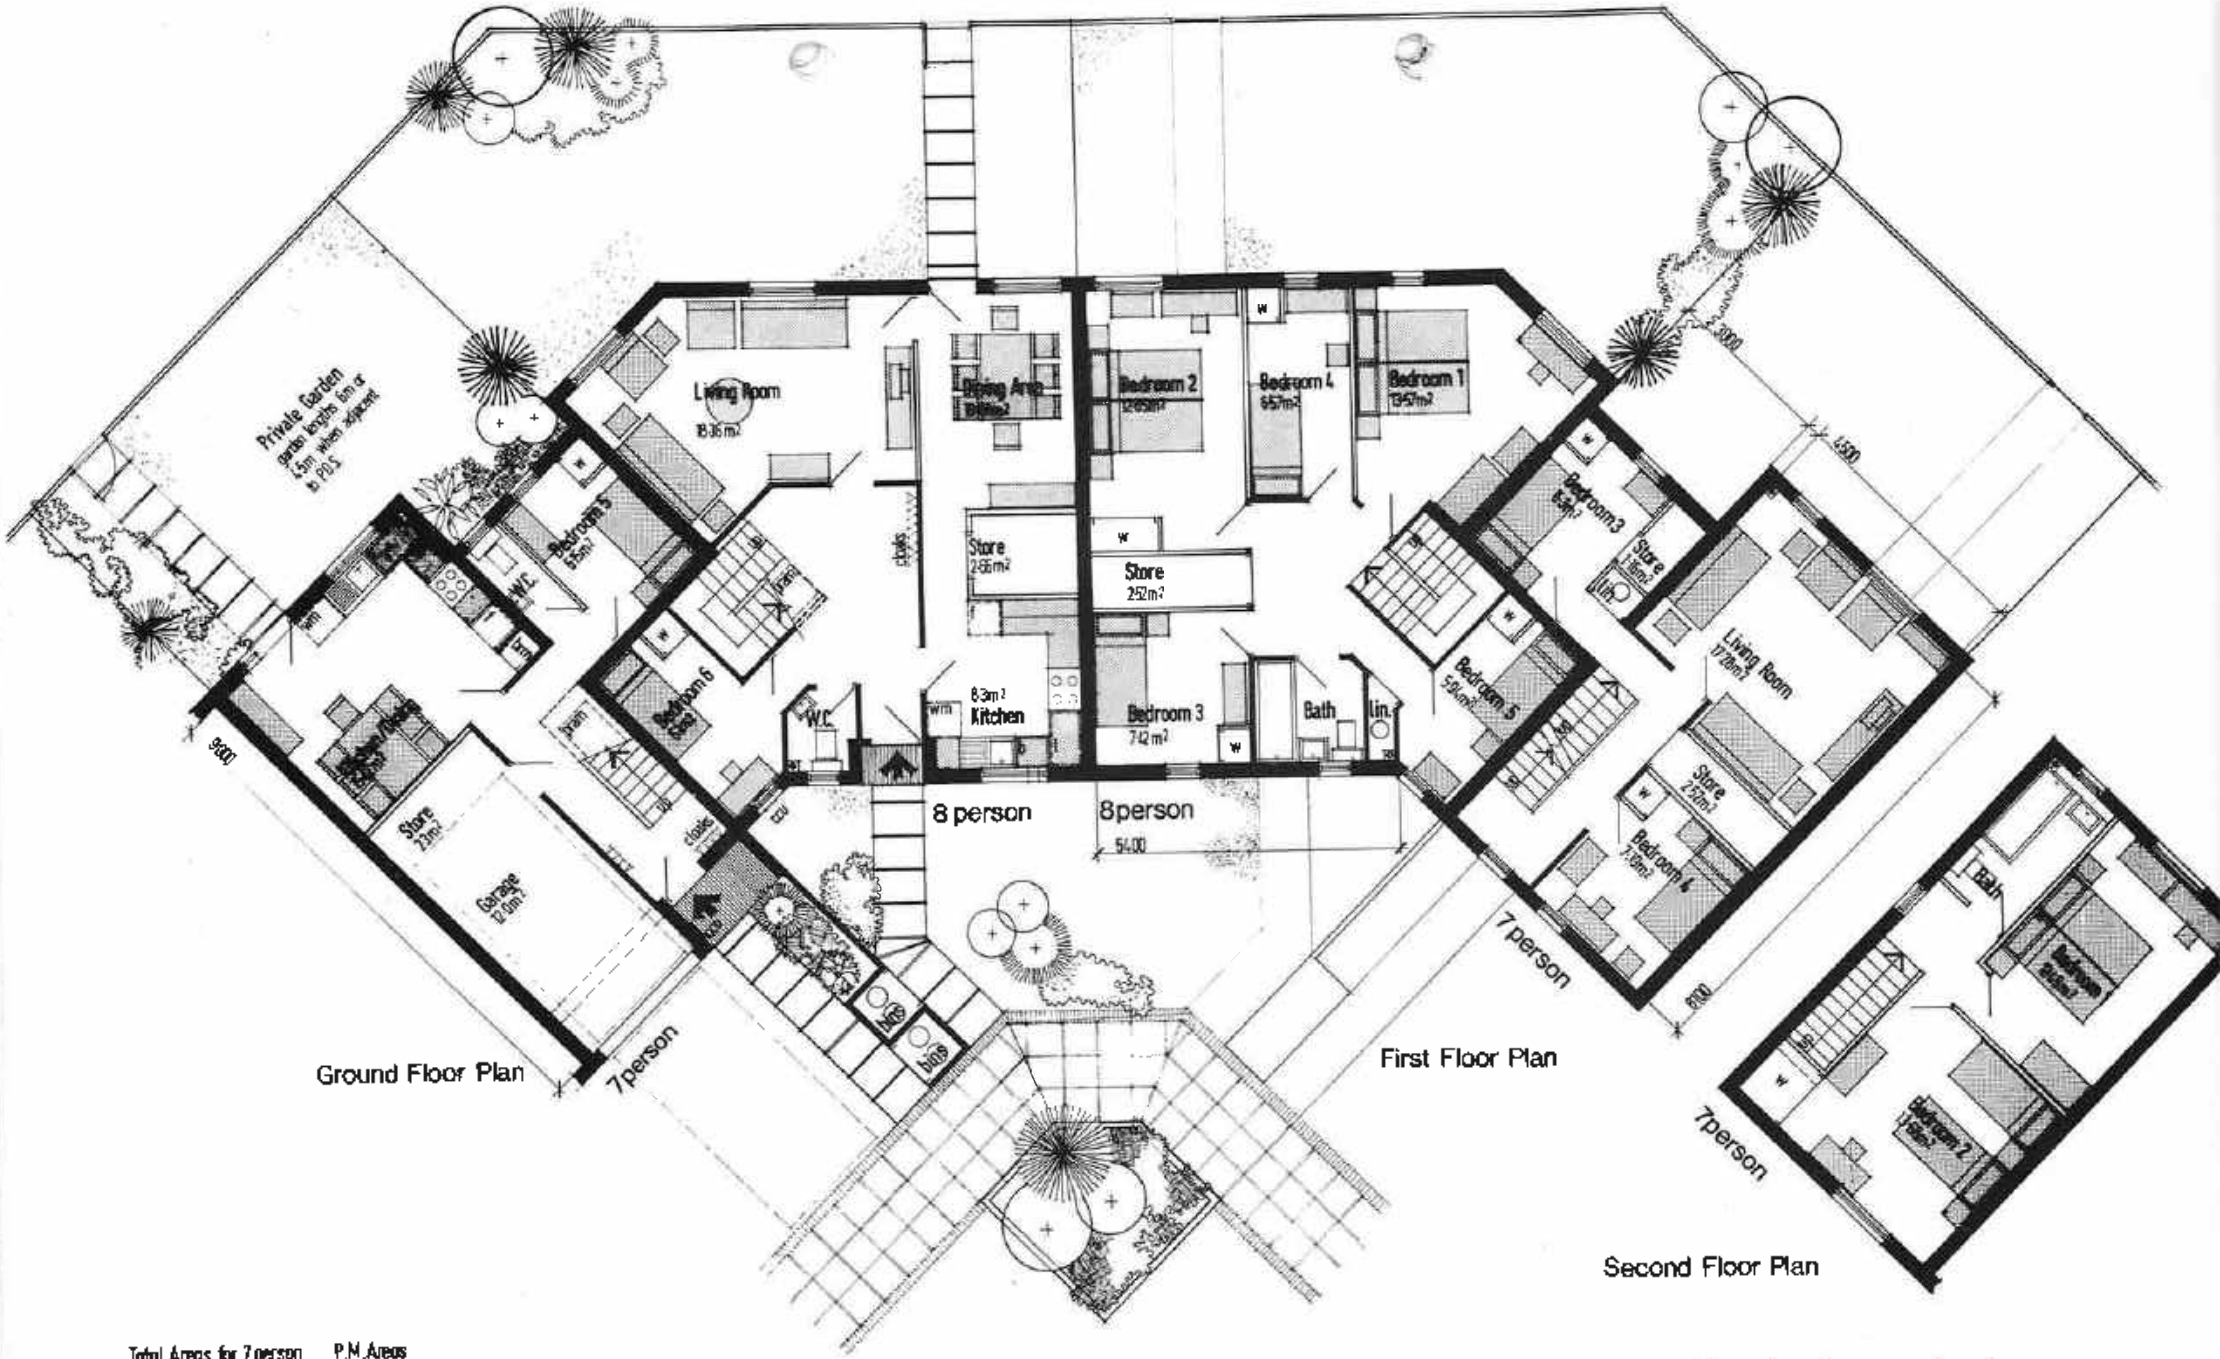

Total Areas for 7 person		P.M. Areas
Gross overall	117·45m²	118·5m²
Net space	113·87m²	112·0m²
Storage	5·98m²	6·5m²

Total Areas for 8 person		
Gross overall	132·94m²	139·5m²
Net space	126·86m²	133·0m²

Key wm · washing machine
l · larder f · fridge b · boiler
brms · brooms ecu · elect. meter
non-structural partition

7+8 person houses

THAMESMEAD AREA 10
DATE: AUGUST 1975
SCALE: 1:50
DRG NO. 9162/20/TSA

Thamesmead has been designed by the Greater London Council Department of Architecture and Civic Design, Architect to the Council and Controller of Construction Services, Sir Roger Walters, KBE, FRIBA, FIStructE (in succession to Sir Hubert Bennett).

The following officers have been responsible for:

Housing and ancillary facilities
Special Works Architect and Thamesmead Manager, Geoffrey Horsfall

Divisional Architect, Thamesmead Division
Eric Hayes
(in succession to J G H D Cairns)

Schools and Educational Facilities for the Inner London Education Authority
Education Architect, Peter E Jones

Consultant Services

Civil Engineering
The Housing Engineer (GLC) R P Manning-Coe

Structural Engineering
The Structural Engineer (GLC) E W Bunn

Quantity Surveying
The Quantity Surveyor (GLC) H S Page

Officers from other GLC departments who have also been responsible are:

The Chief Officer of the Parks Department, J C Kennedy
The Director of Mechanical and Electrical Engineering, P C Hoare
The Controller of Planning and Transportation, F B Pooley
The Valuer and Estates Surveyor, K M Blessley
The Controller of Housing, H G Simpson

FURTHER INFORMATION

A detailed bibliography (Research Bibliography No. 62 June 1975) has been compiled by the GLC Research Library and is available from the GLC Bookshop, The County Hall, London SE1 7PB, price 40 pence.


Other brochures in this series are:

Thamesmead - An Introduction
Thamesmead - The First Areas

and these are available from the address below.

All enquiries about the work of the GLC Department of Architecture and Civic Design should be addressed to:

The Information Officer
GLC Department of Architecture and Civic Design
Room 179 North Block
The County Hall
London
SE1 7PB

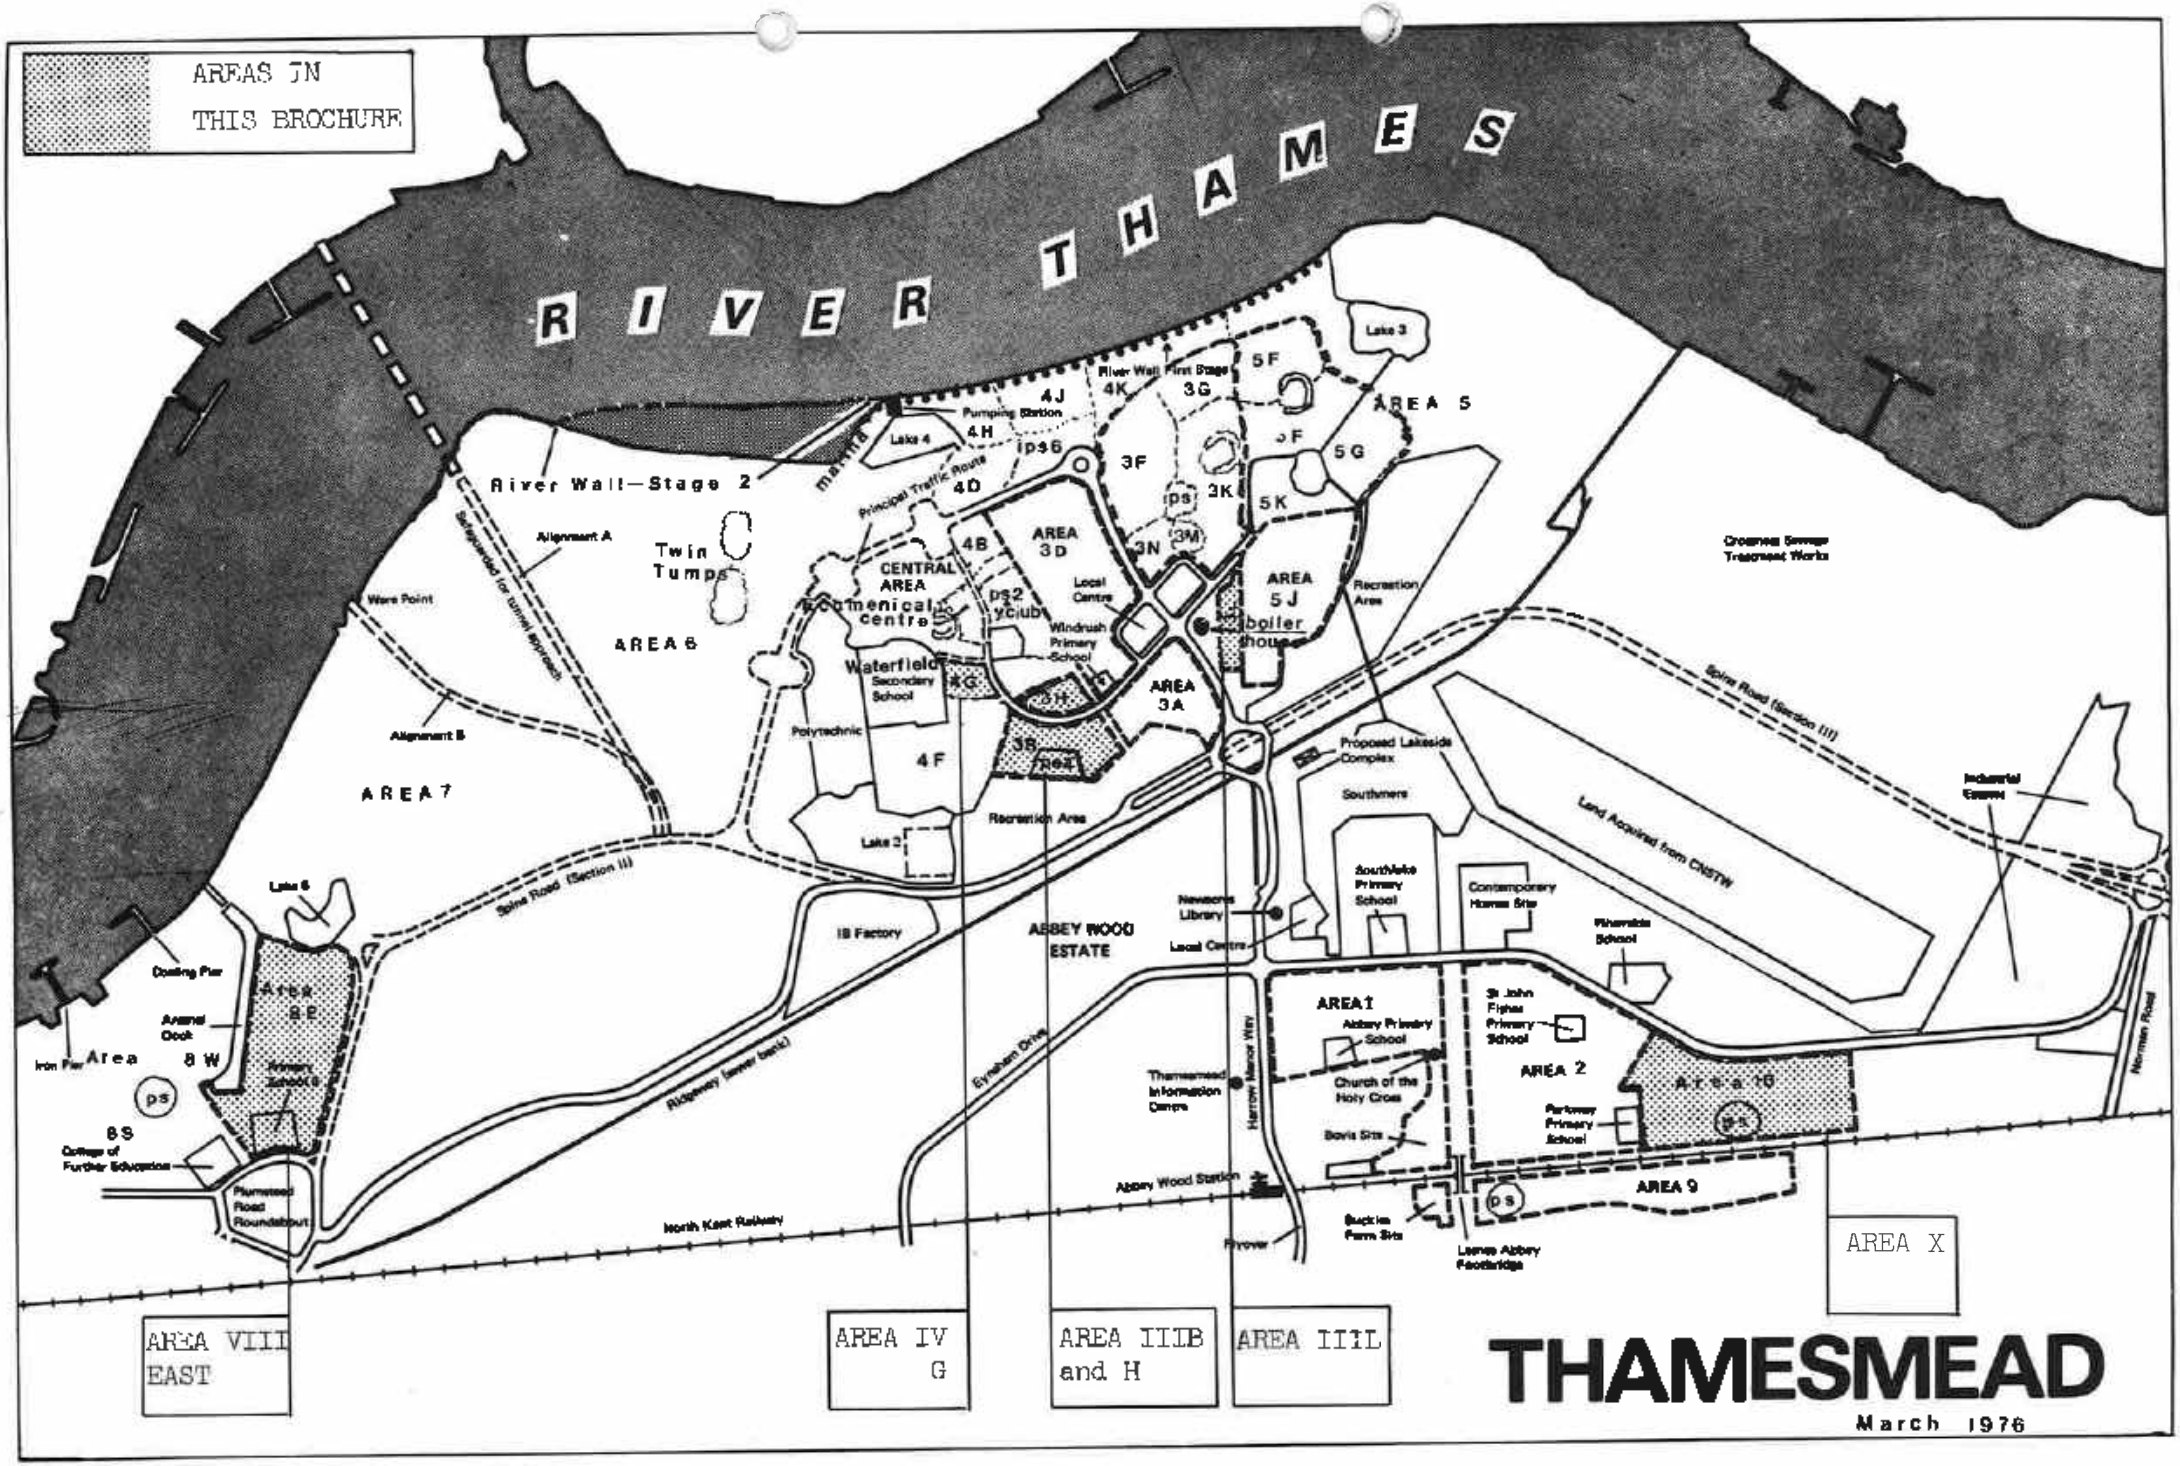
AREAS IN THIS BROCHURE
RIVER THAMES
River Wall—Stage 2
Alignment A
Alignment B
Twin Tumps
Ware Point
AREA 6
AREA 7
CENTRAL AREA
Ecumenical centre
Waterfield Secondary School
Polytechnic
Windrush Primary School
Local Centre
AREA 3D
AREA 3A
AREA 5J
boiler house
Recreation Area
Lake 2
Lake 3
Lake 4
Lake 5
Lake 6
AREA 5
Crossness Sewage Treatment Works
Proposed Lakeside Complex
Southmere
Land Acquired from CNSTW
Spine Road (Section III)
Industrial Estate
Southlake Primary School
Contemporary Homes Site
Wheatside School
Newsome Library
Local Centre
ABBEY WOOD ESTATE
IB Factory
Area 8E
Area 8W
Area 8S
Area 10
AREA 1
Abbey Primary School
Church of the Holy Cross
Boris Site
St John Fisher Primary School
AREA 2
Parkway Primary School
AREA 9
Abbey Wood Station
North East Railway
Thamesmead Information Centre
Harrow Manor Way
Eynsham Drive
Ridgeway (sewer tank)
Plumstead Road Roundabout
College of Further Education
Arsenal Dock
Iron Pier
Dowding Pier
Primary School
Buckles Farm Site
Lesnes Abbey Footbridge
Norman Road
AREA VIII EAST
AREA IV G
AREA IIIB and H
AREA IIIL
AREA X
THAMESMEAD
March 1976